


01 Planta Baixa e Locação
Escala 1:50
Unidades: cm

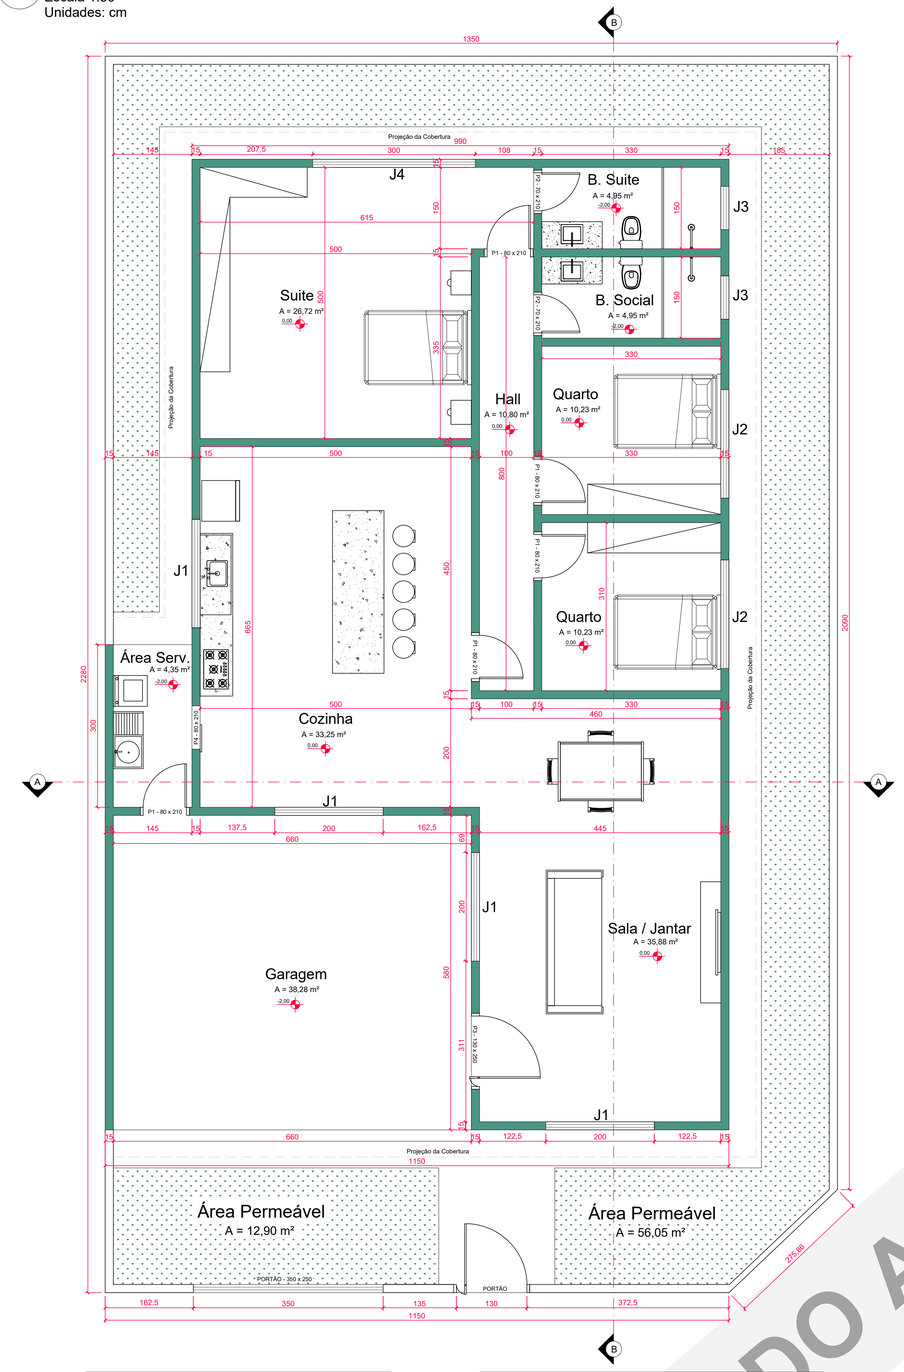


02 Planta de Cobertura
Escala 1:100
Unidades: cm

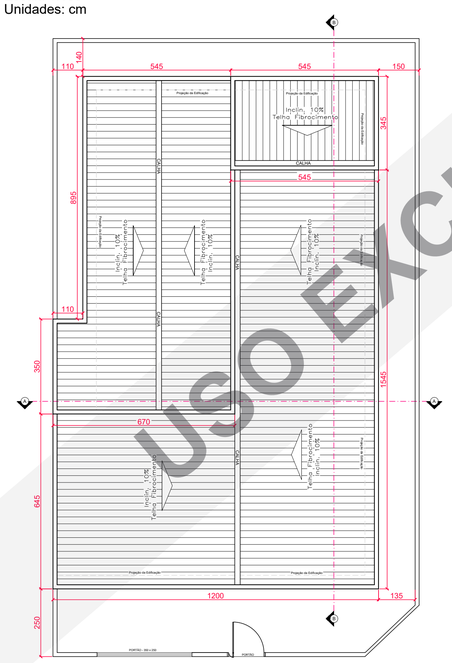

03 Corte BB
Escala 1:50
Unidades: cm

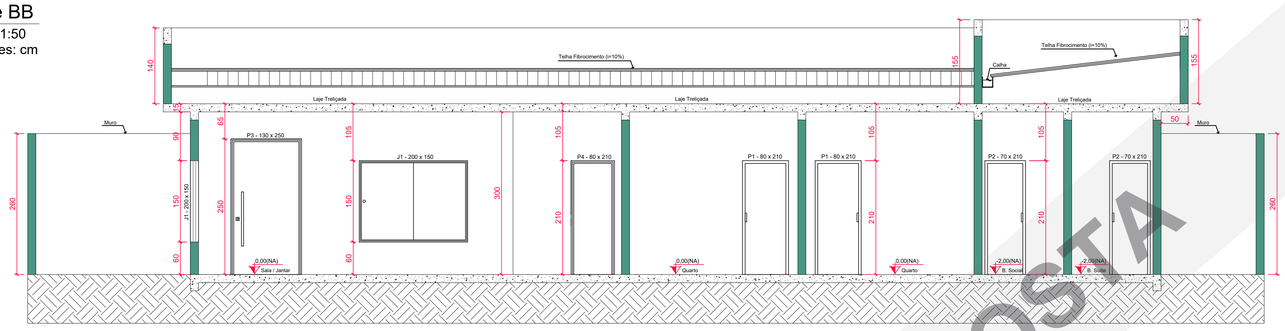

04 Corte AA
Escala 1:50
Unidades: cm

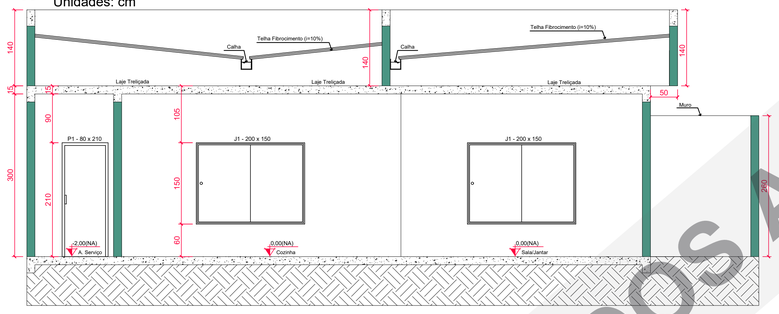


QUADRO DE ESQUADRIAS						
LEGENDA	QUANT.	LARGURA	ALTURA	PEITORIL	MATERIAL	TIPO
P1	05	80	210	–	MADEIRA	ABRIR
P2	02	70	210	–	MADEIRA	ABRIR
P3	01	130	250	–	MADEIRA	ABRIR
P4	01	80	210	–	MADEIRA	CORRER
J1	04	200	150	60	VIDRO	CORRER
J2	02	200	100	90	VIDRO	CORRER
J3	02	80	80	130	VIDRO	BASCULAN.
J4	01	300	150	60	VIDRO	CORRER


05 Vista Lateral Esquerda
Escala 1:50
Unidades: cm




06 Vista Lateral Direita
Escala 1:50
Unidades: cm

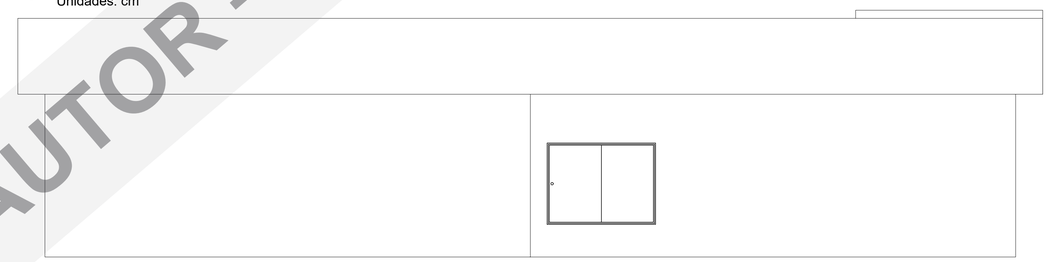


07 Vista Fundo
Escala 1:50
Unidades: cm

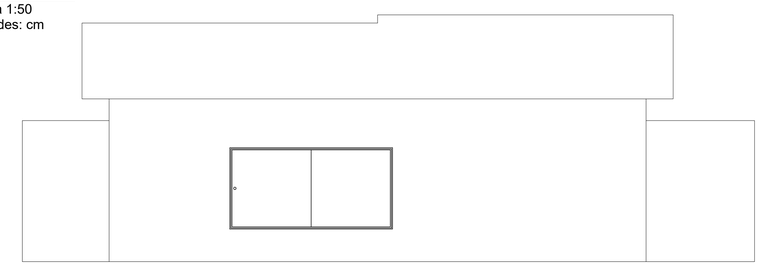

08 Vista Frontal
Escala 1:50
Unidades: cm

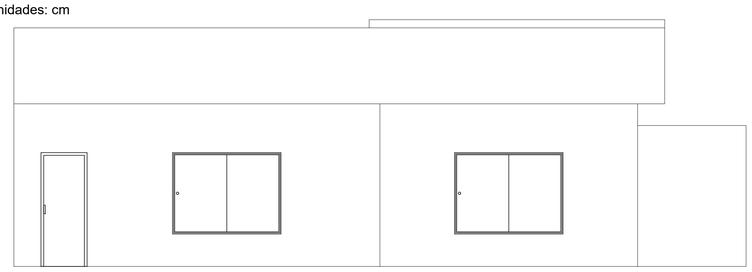

09 Planta de Situação
Escala 1:500
Unidades: cm

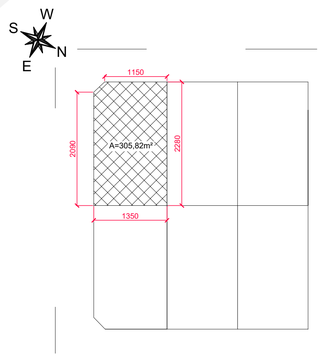

LEGENDA

- Área de Permeabilidade = 68,95 m²

Obs.: A área destinada a permeabilidade recoberta com grama esmeralda, brita e/ou o próprio recobrimento natural do solo.

USO EXCLUSIVO DO AUTOR — GABRIEL DOS ANJOS COSTA