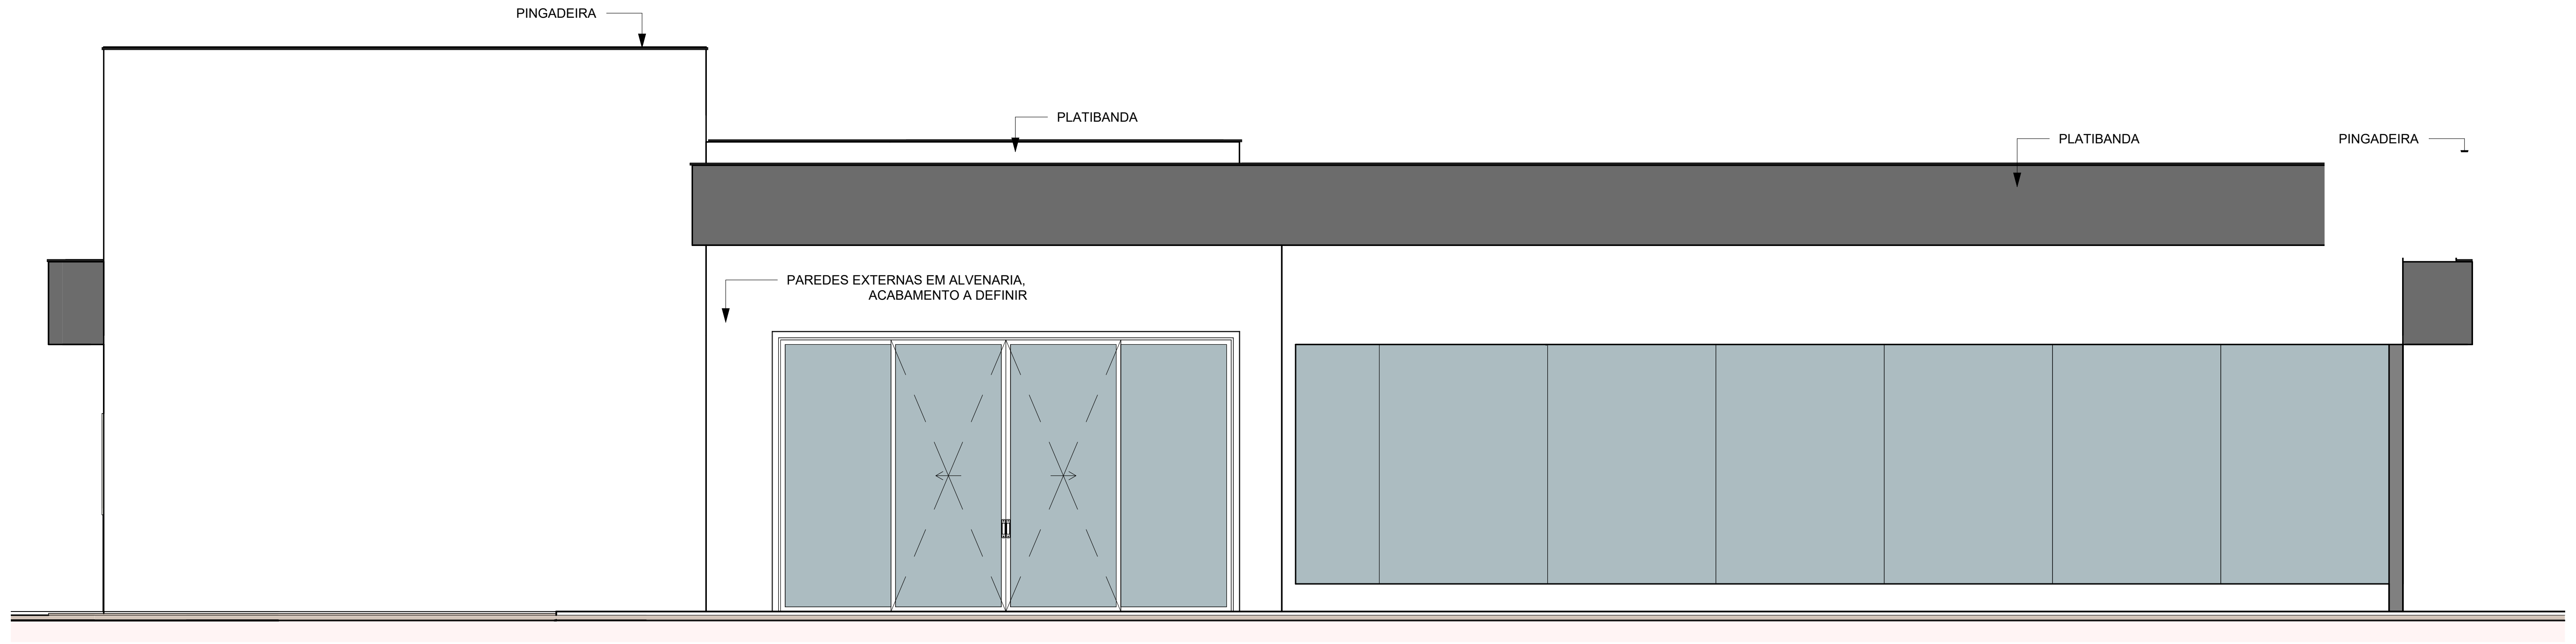

1 ELEVAÇÃO FRONTAL

1 : 50

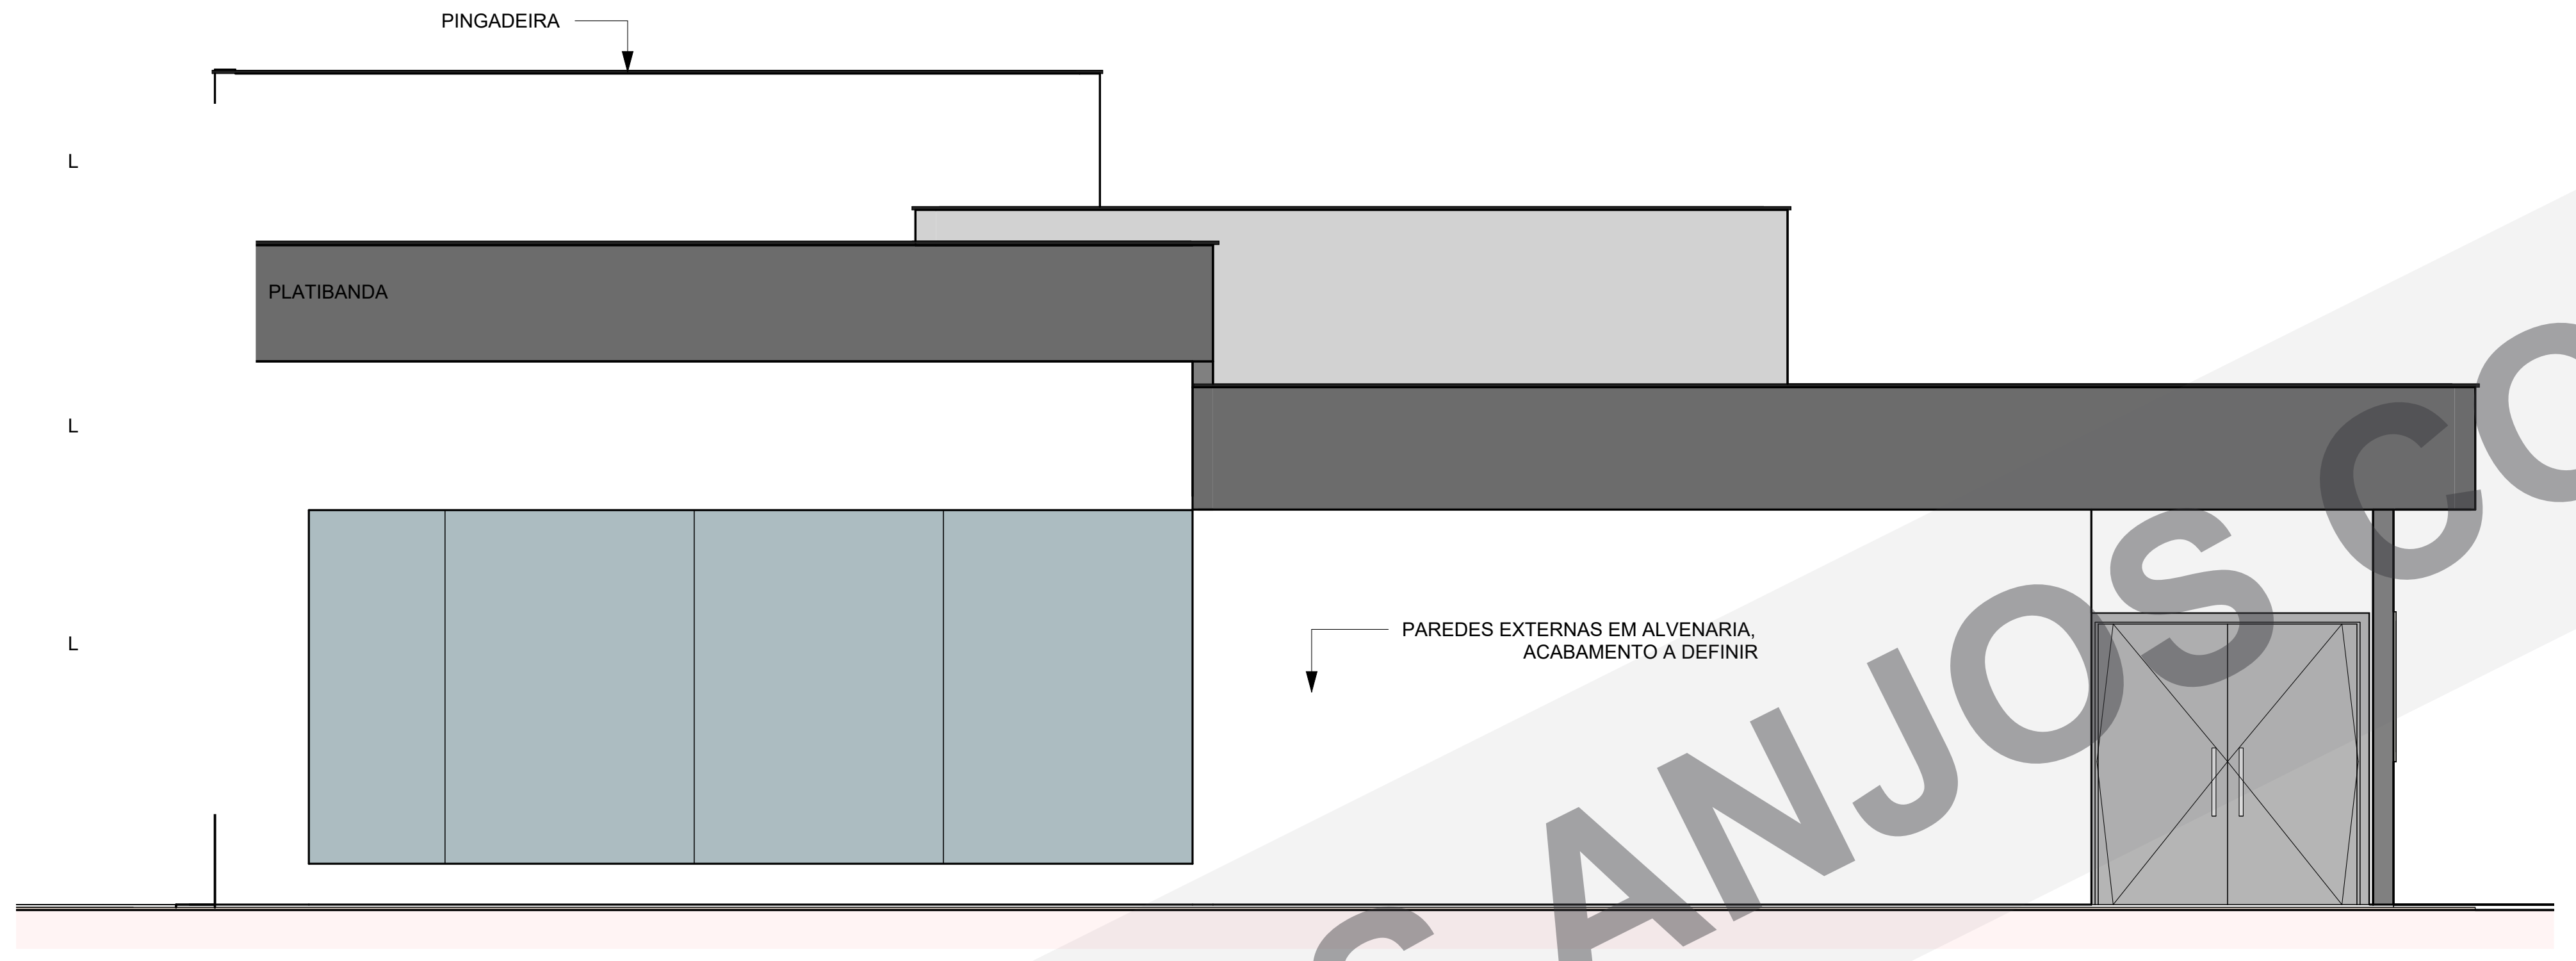

5 ELEVAÇÃO DIREITA

1 : 50

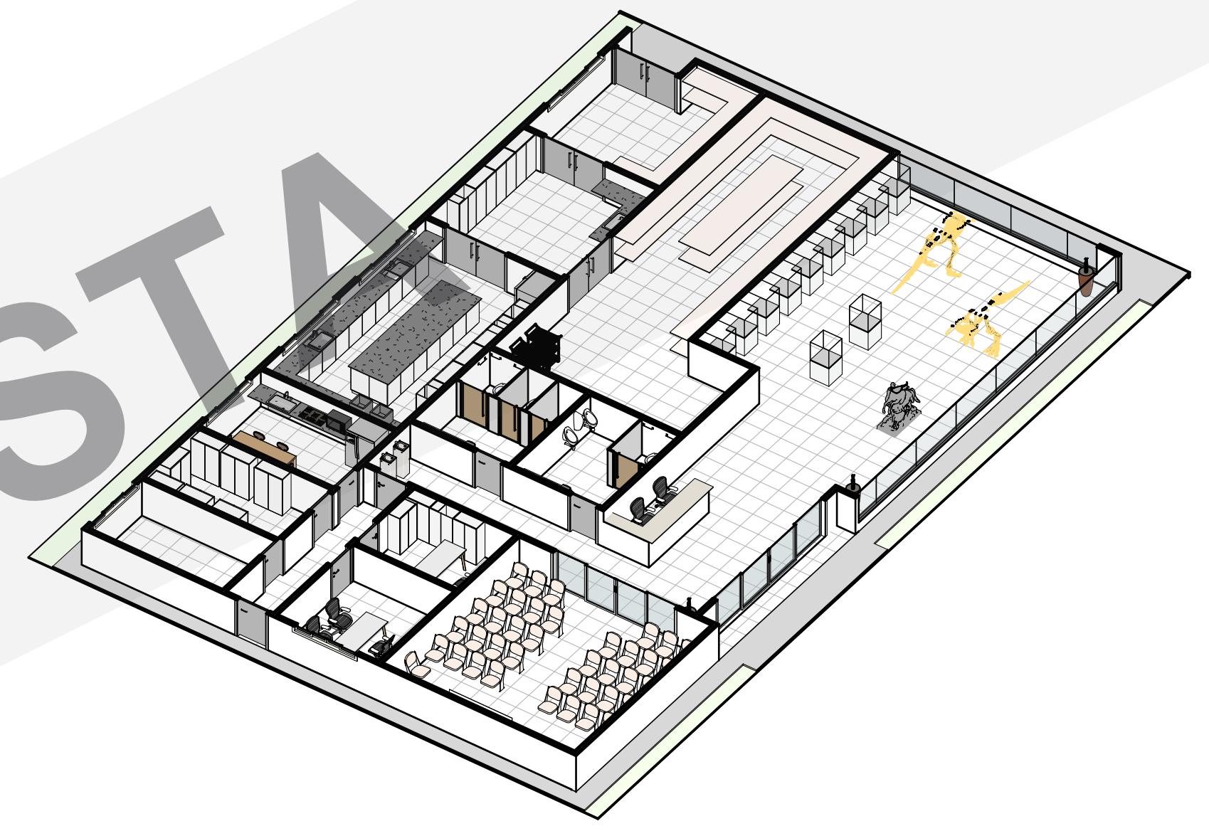

7 CORTE ESQUEMÁTICO

QUADRO DE JANELAS					
CÓDIGO	LARGURA	ALTURA	A. PEITORIL	TIPO / MATERIAL	QUANT.
J1	250	100	110	CORRER 4F/VIDRO	3
J2	200	100	110	CORRER 4F/VIDRO	3

QUADRO DE PORTAS				
CÓDIGO	LARGURA	ALTURA	TIPO / MATERIAL	QUANT.
P1	200	210	ABRIR 2F/MADEIRA	4
P2	90	180	ABRIR/ALUMÍNIO	2
P3	70	180	ABRIR/ALUMÍNIO	2
P4	90	210	ABRIR/MADEIRA	7
P5	100	210	ABRIR/MADEIRA	2
P6	500	300	CORRER 4F/VIDRO	1
P7	400	210	CORRER 4F/VIDRO	1

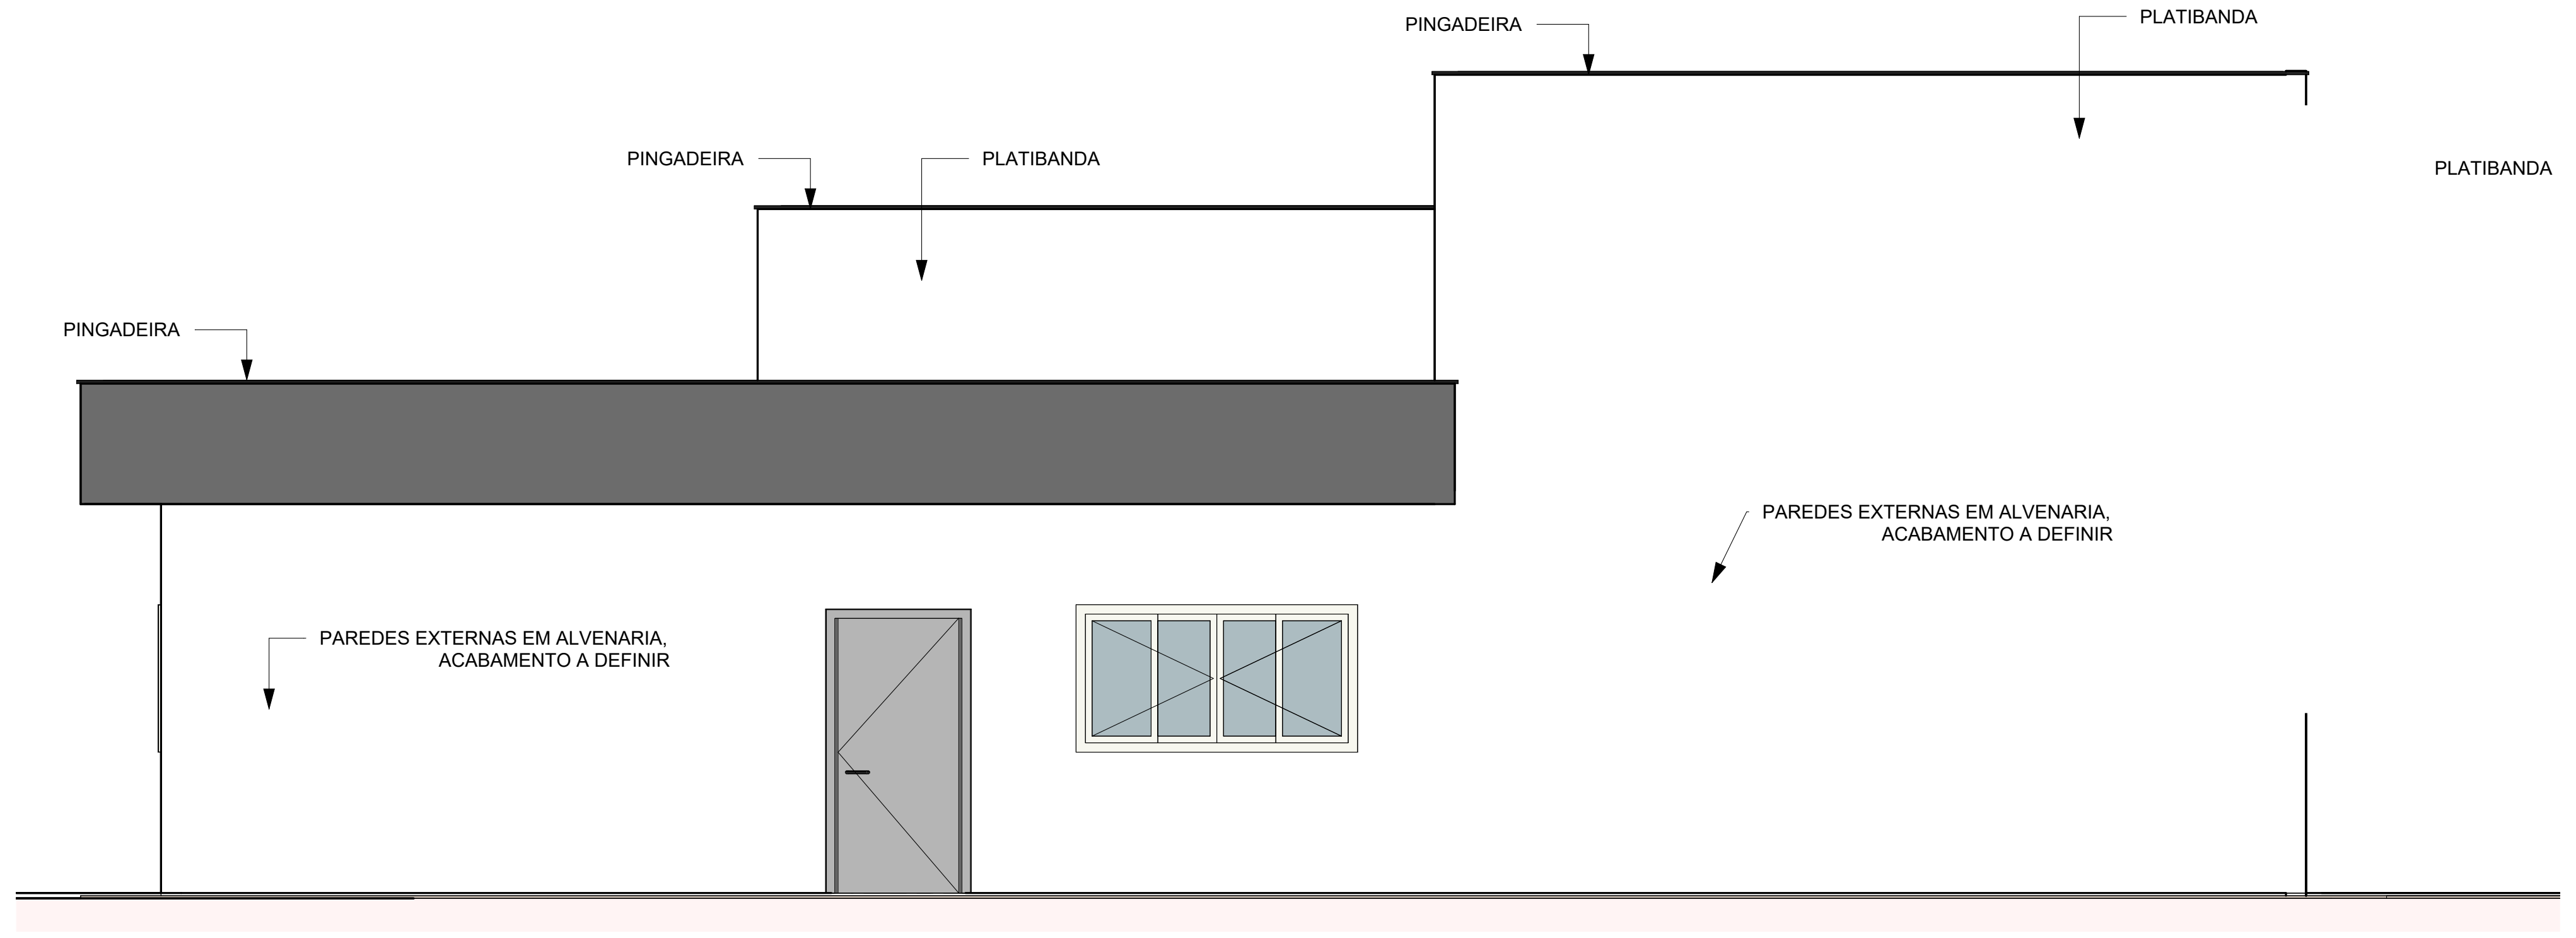
PINGADEIRA
PLATIBANDA
PINGADEIRA
PLATIBANDA
PINGADEIRA
PLATIBANDA
PAREDES EXTERNAS EM ALVENARIA, ACABAMENTO A DEFINIR
PAREDES EXTERNAS EM ALVENARIA, ACABAMENTO A DEFINIR

2 ELEVAÇÃO ESQUERDA

1 : 50

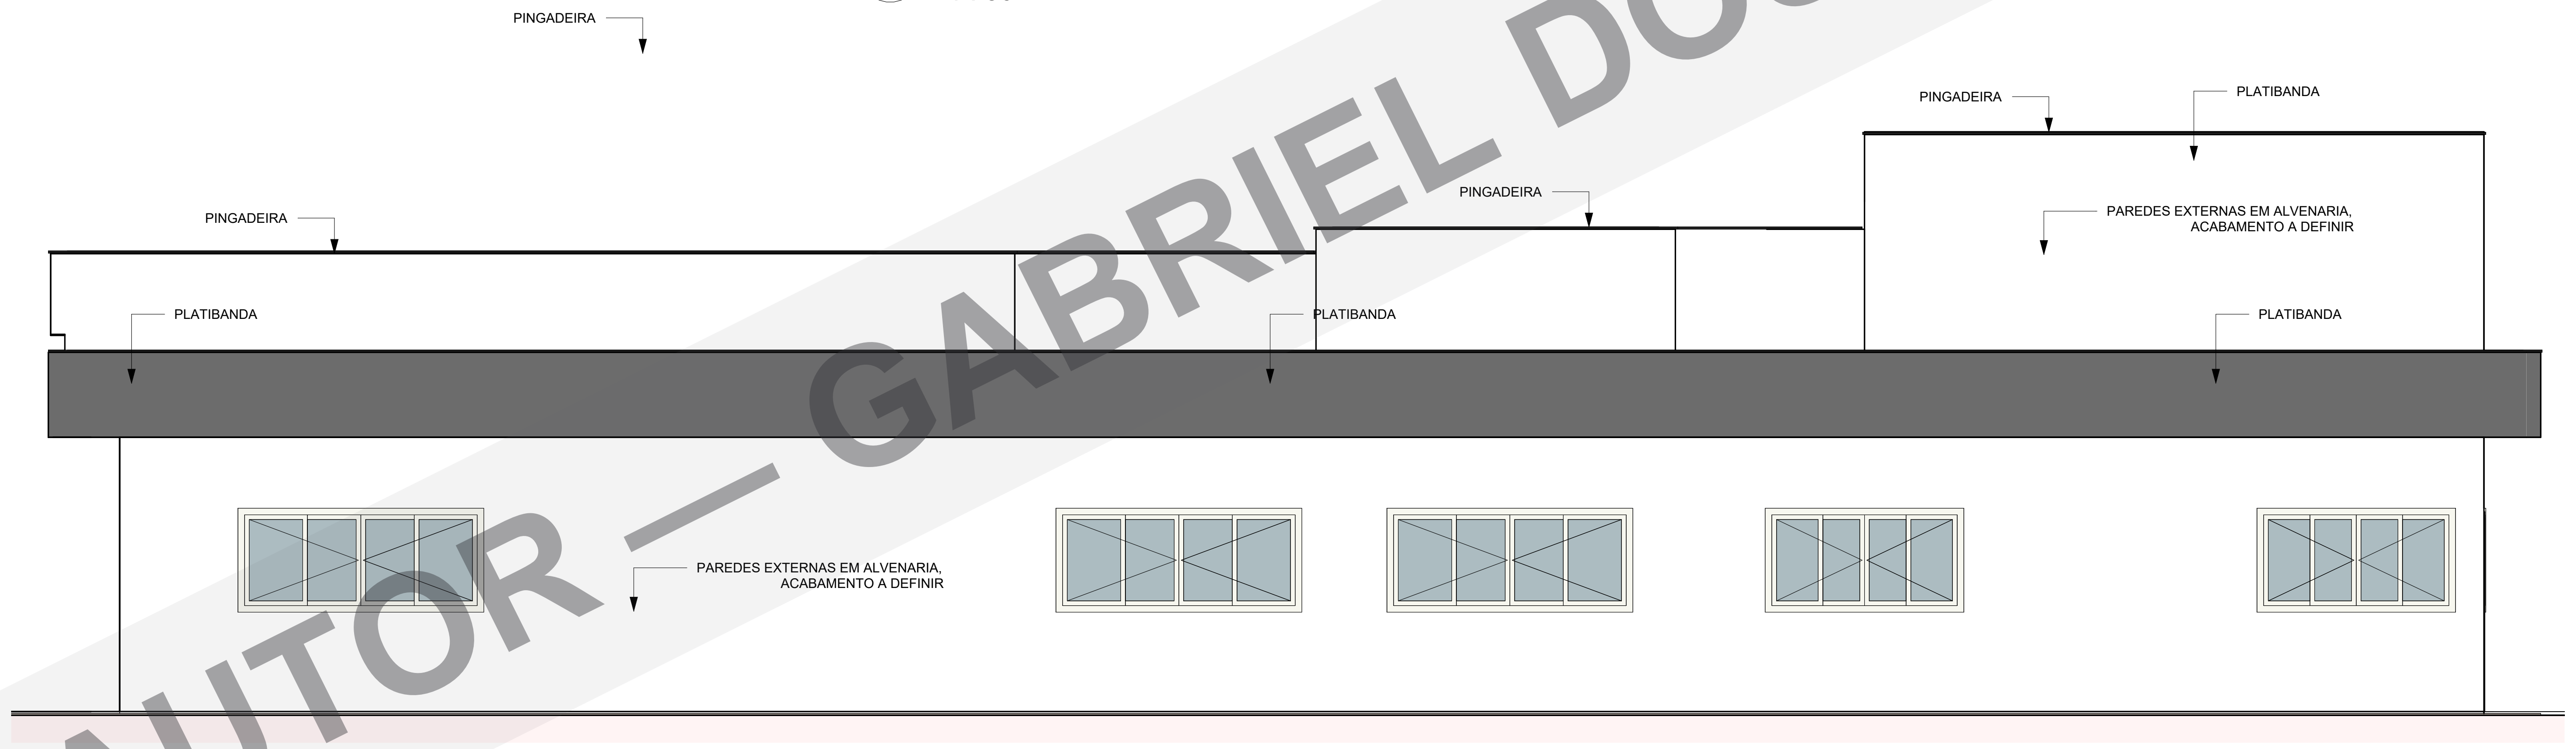
PINGADEIRA
PINGADEIRA
PLATIBANDA
PINGADEIRA
PLATIBANDA
PINGADEIRA
PLATIBANDA
PLATIBANDA
PAREDES EXTERNAS EM ALVENARIA, ACABAMENTO A DEFINIR
PAREDES EXTERNAS EM ALVENARIA, ACABAMENTO A DEFINIR

6 ELEVAÇÃO FUNDO

1 : 50

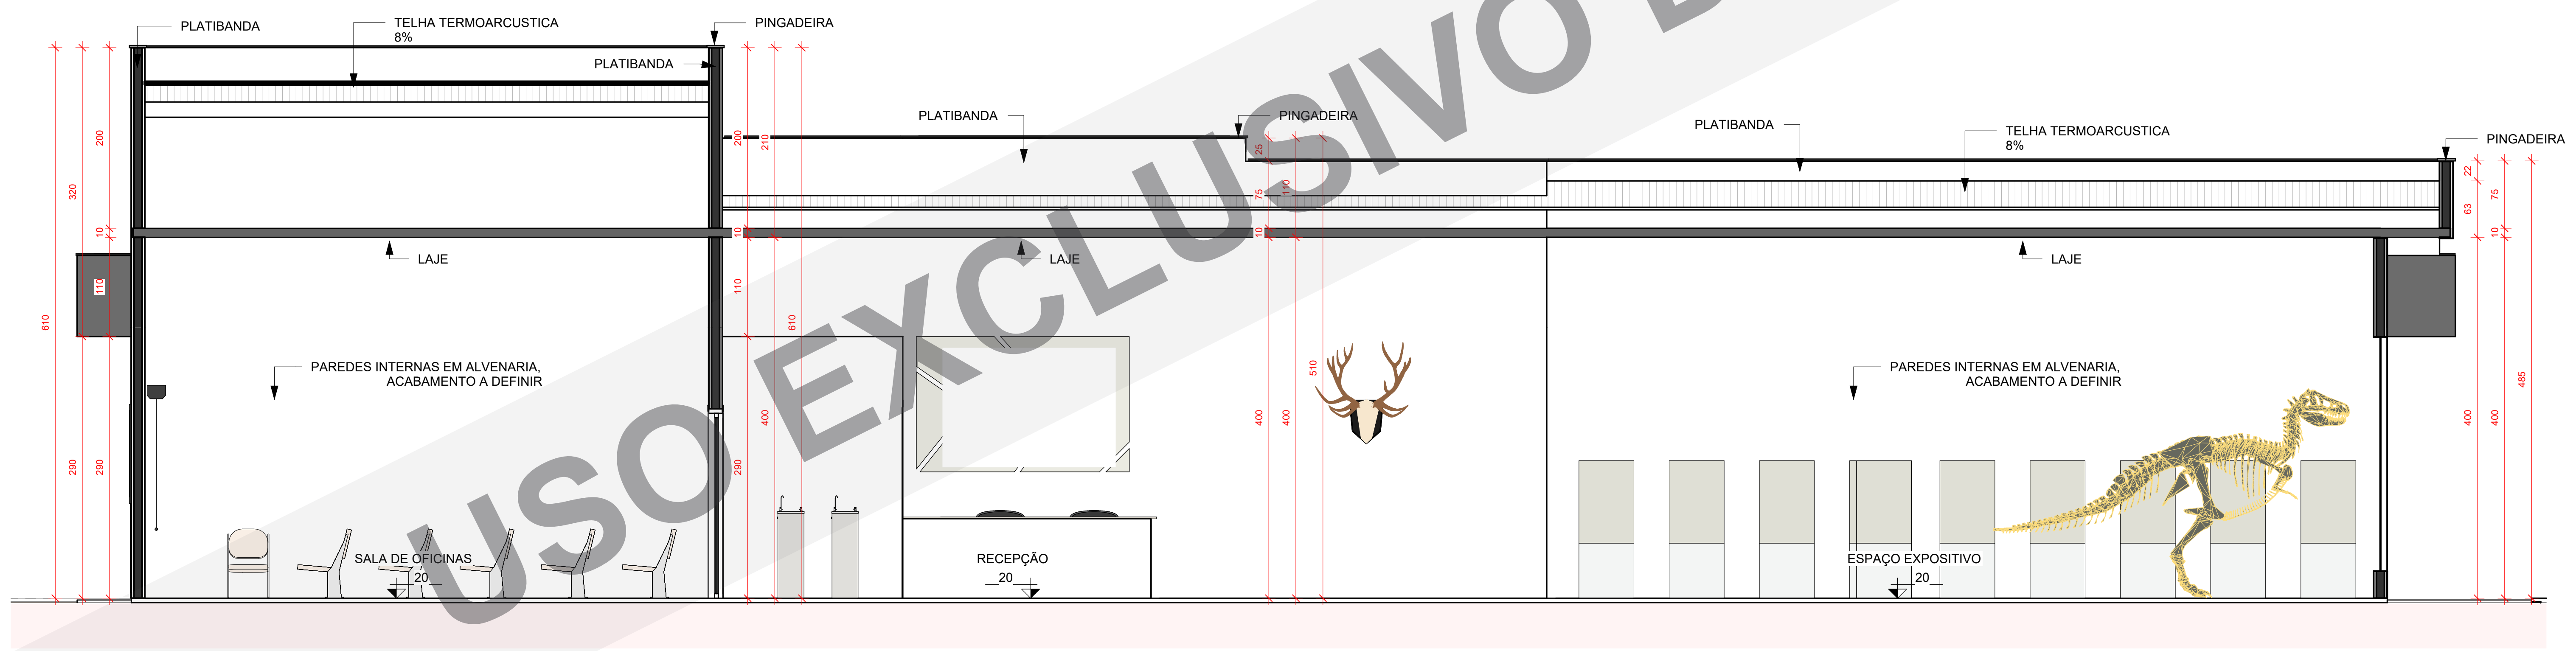

4 CORTE BB

1 : 50

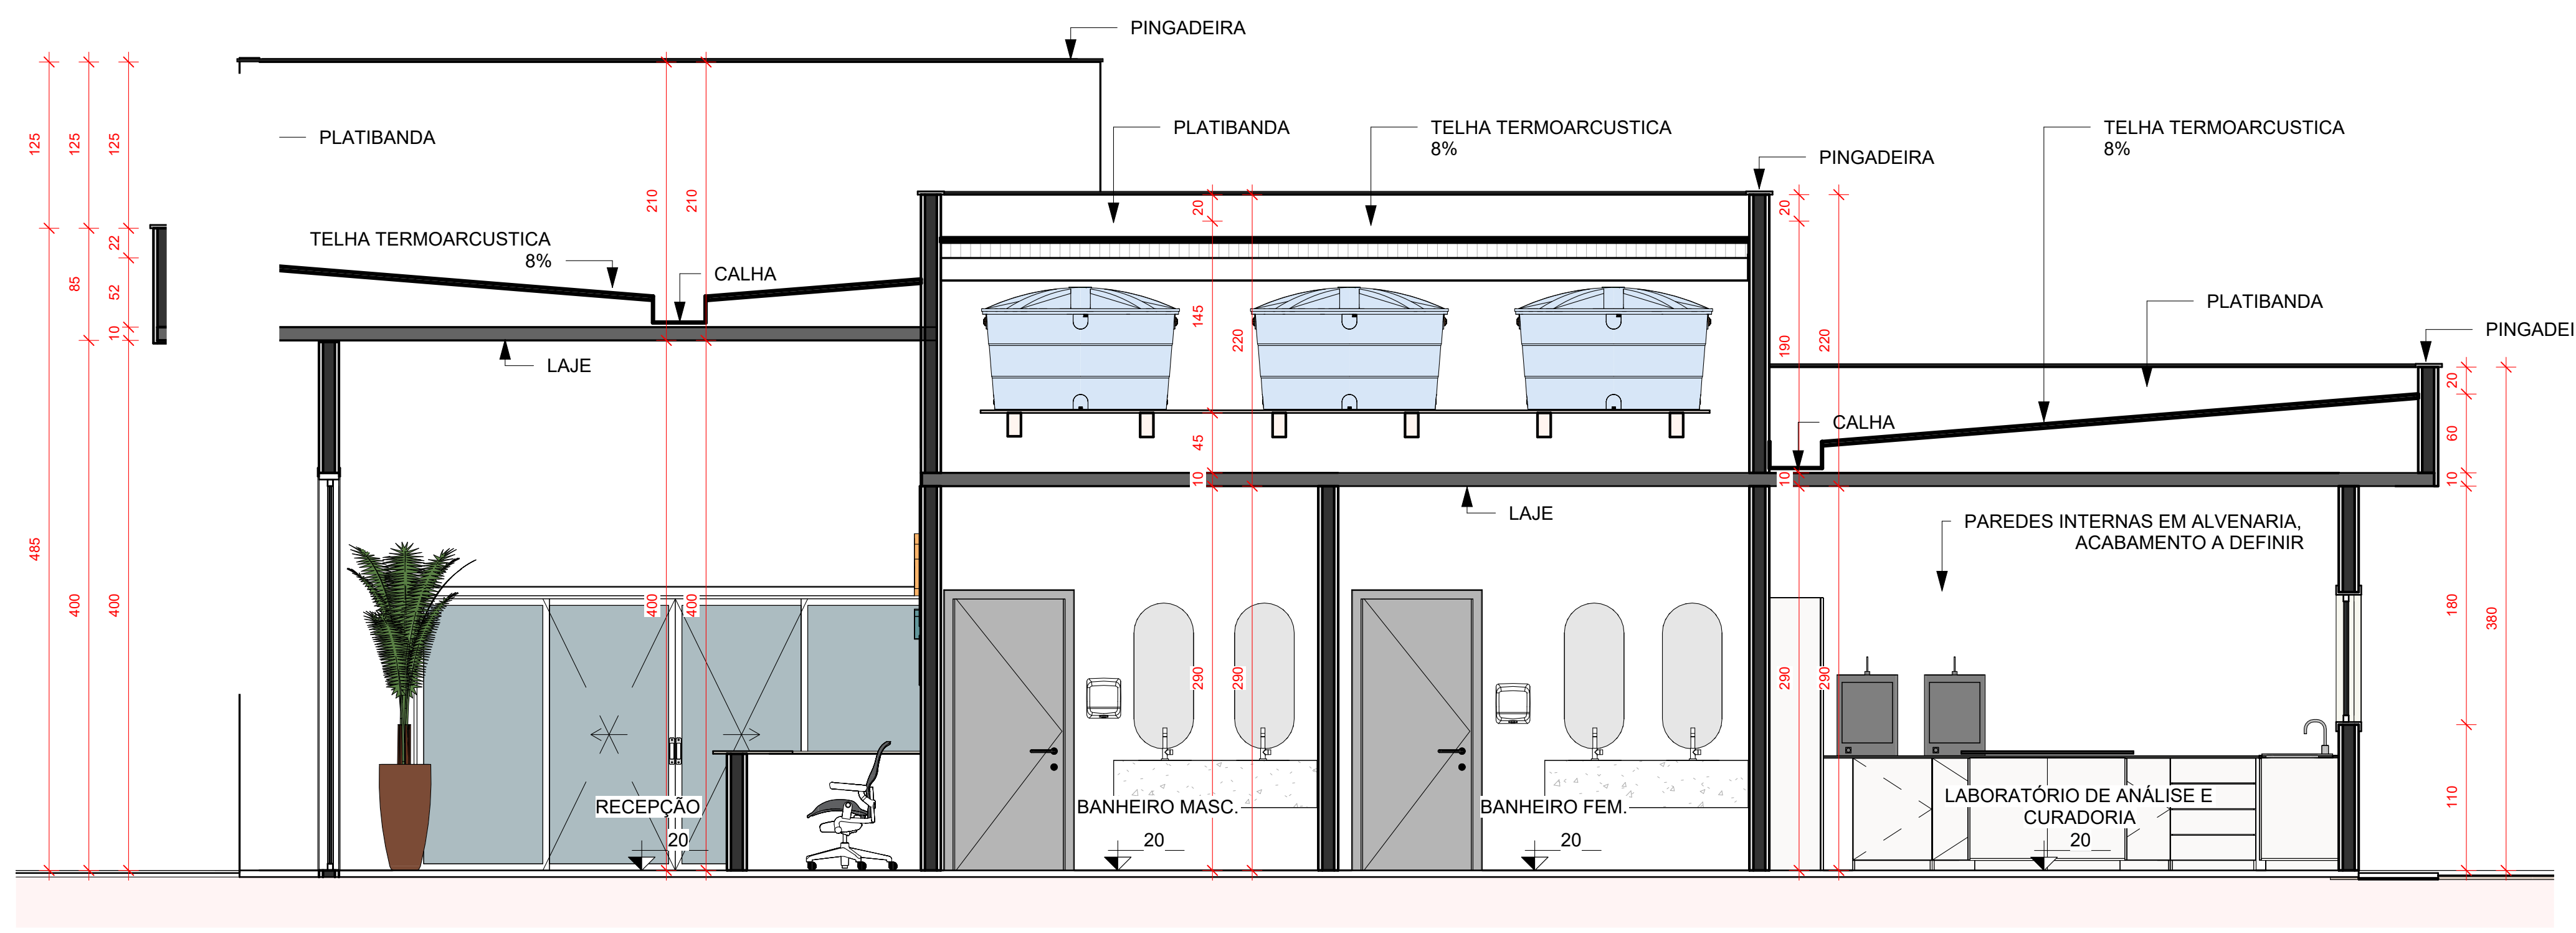

3 CORTE AA

1 : 50

USO EXCLUSIVO DO AUTOR — GABRIEL DOS ANJOS COSTA