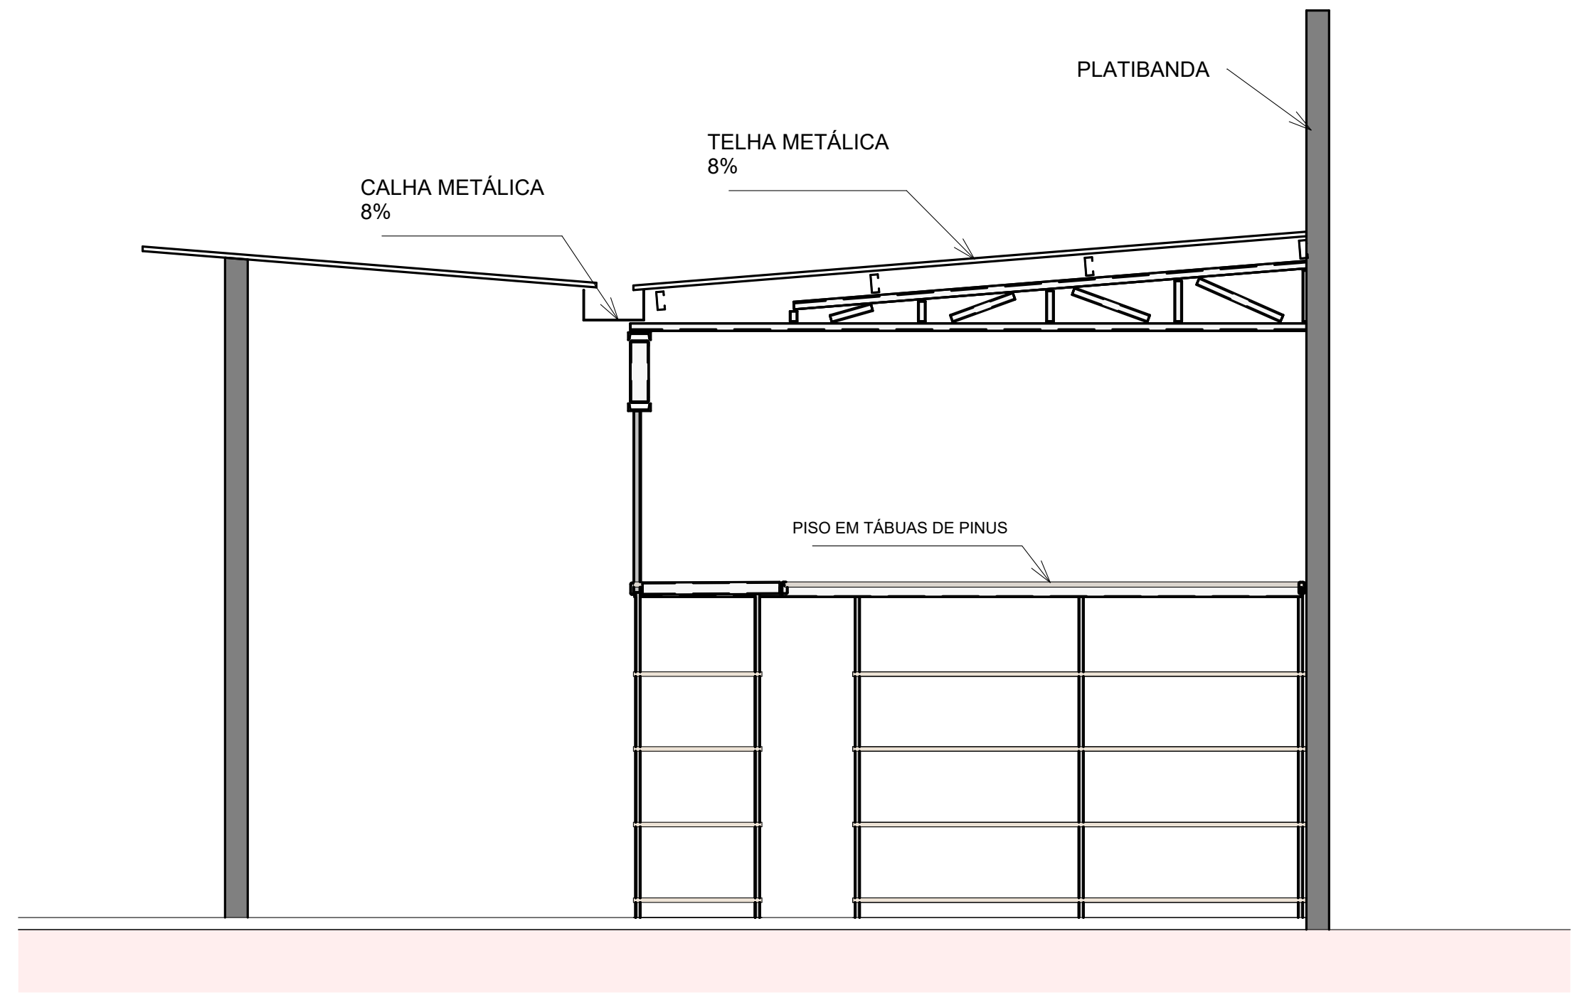
PLATIBANDA
TELHA METÁLICA
8%
CALHA METÁLICA
8%
PISO EM TÁBUAS DE PINUS

5 ELEVAÇÃO DIREITA

1 : 50

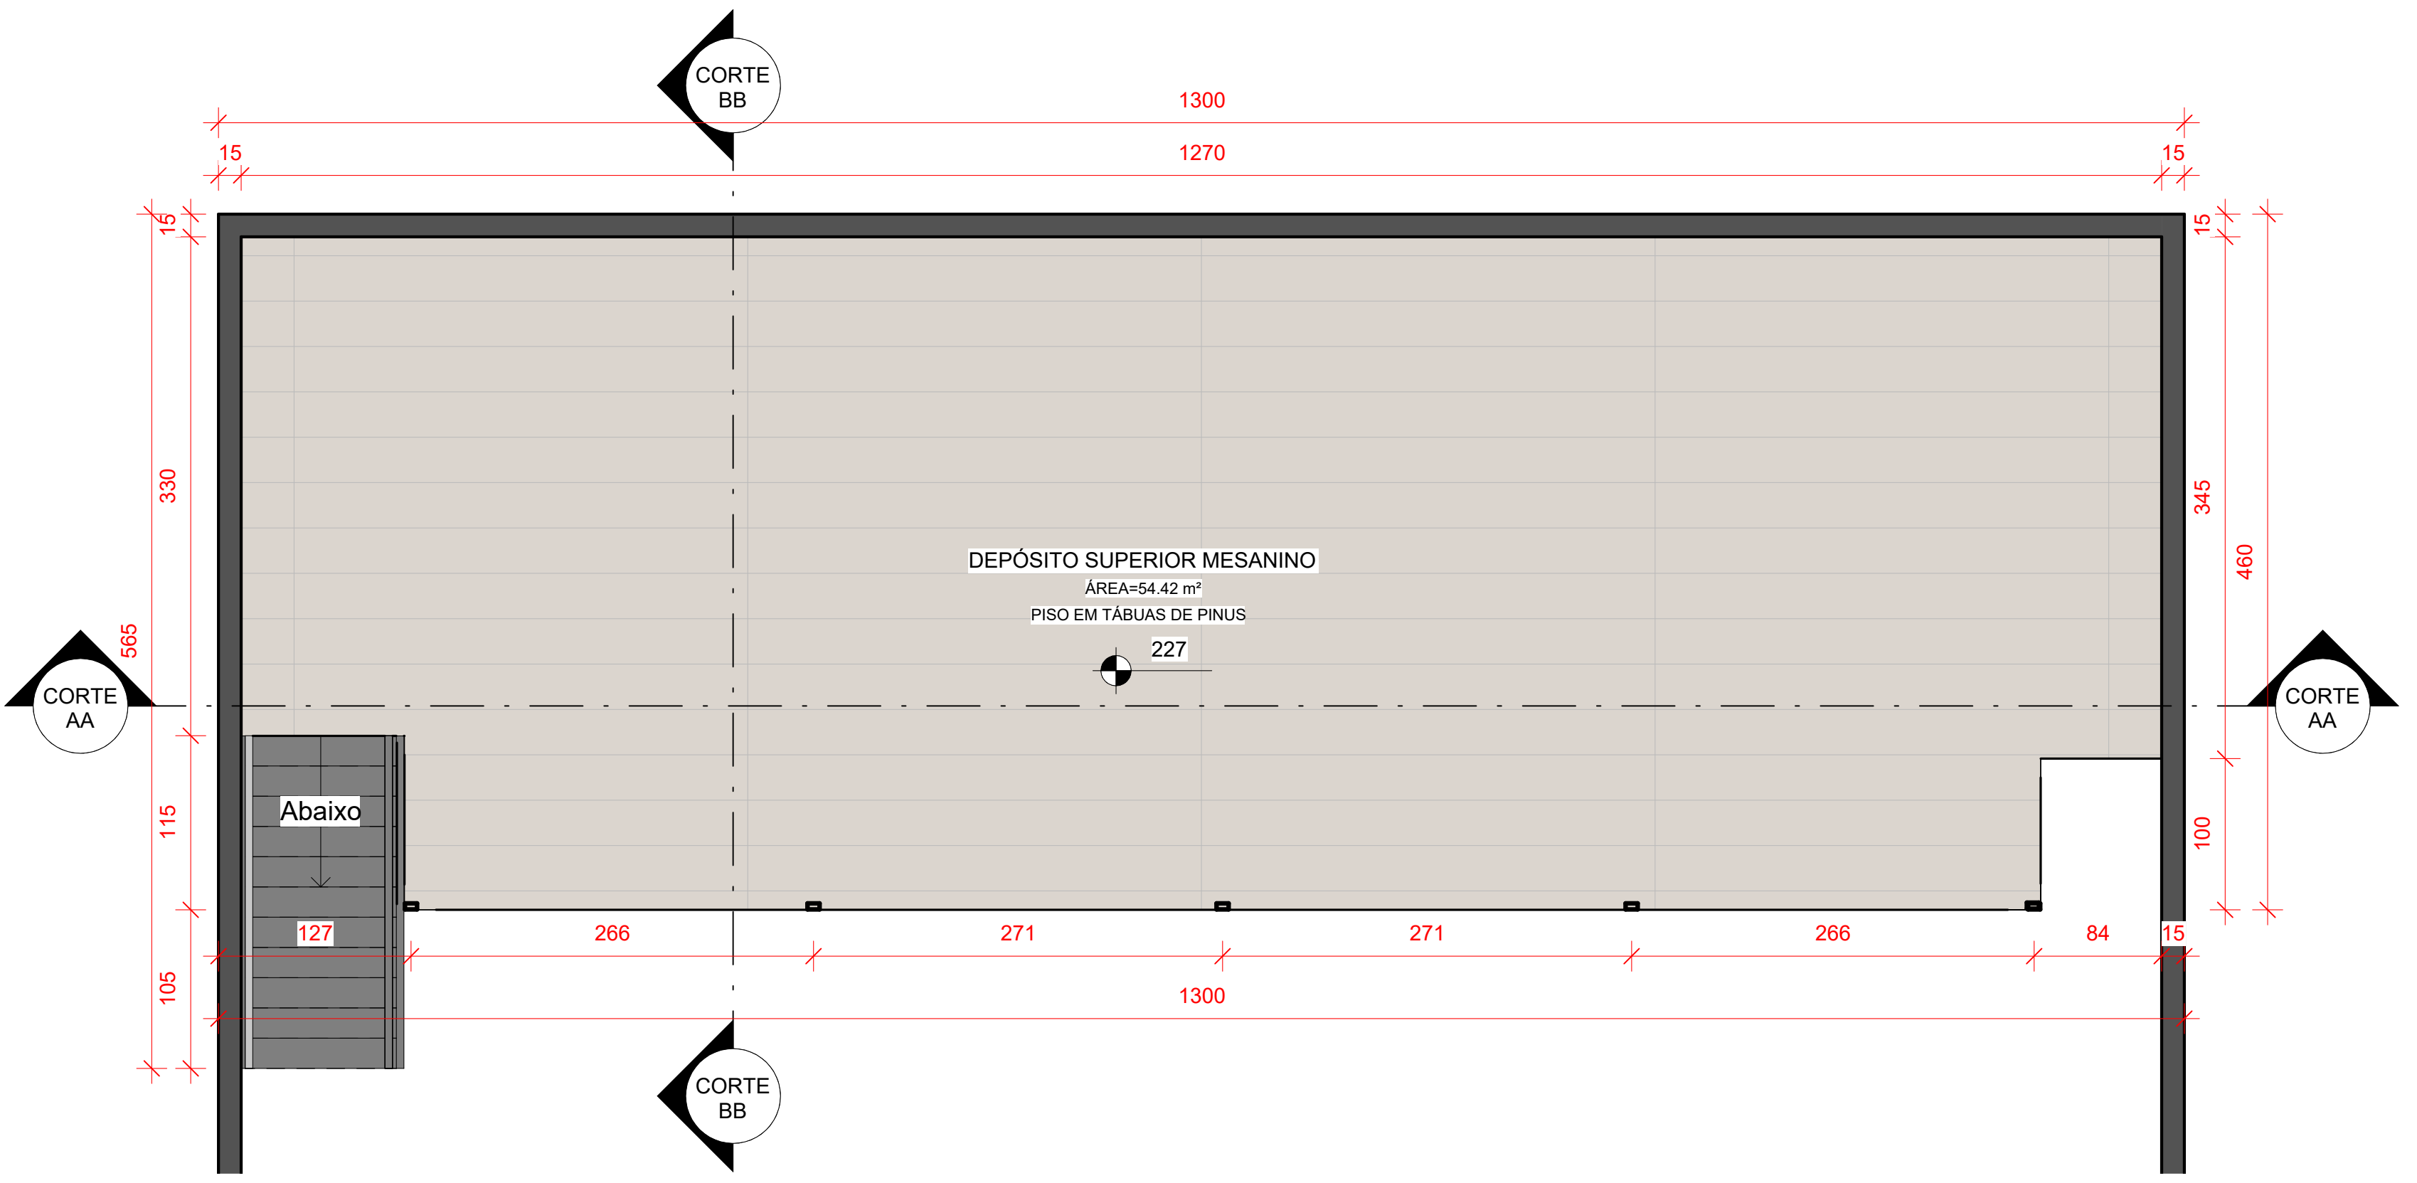
CORTE
BB
1300
15
1270
15
15
330
565
115
105
345
460
100
CORTE
AA
CORTE
AA
DEPÓSITO SUPERIOR MESANINO
ÁREA=54.42 m²
PISO EM TÁBUAS DE PINUS
227
Abaixo
127
266
271
271
266
84
15
1300
CORTE
BB

3 PLANTA BAIXA 1° PAV. MESANINO

1 : 50

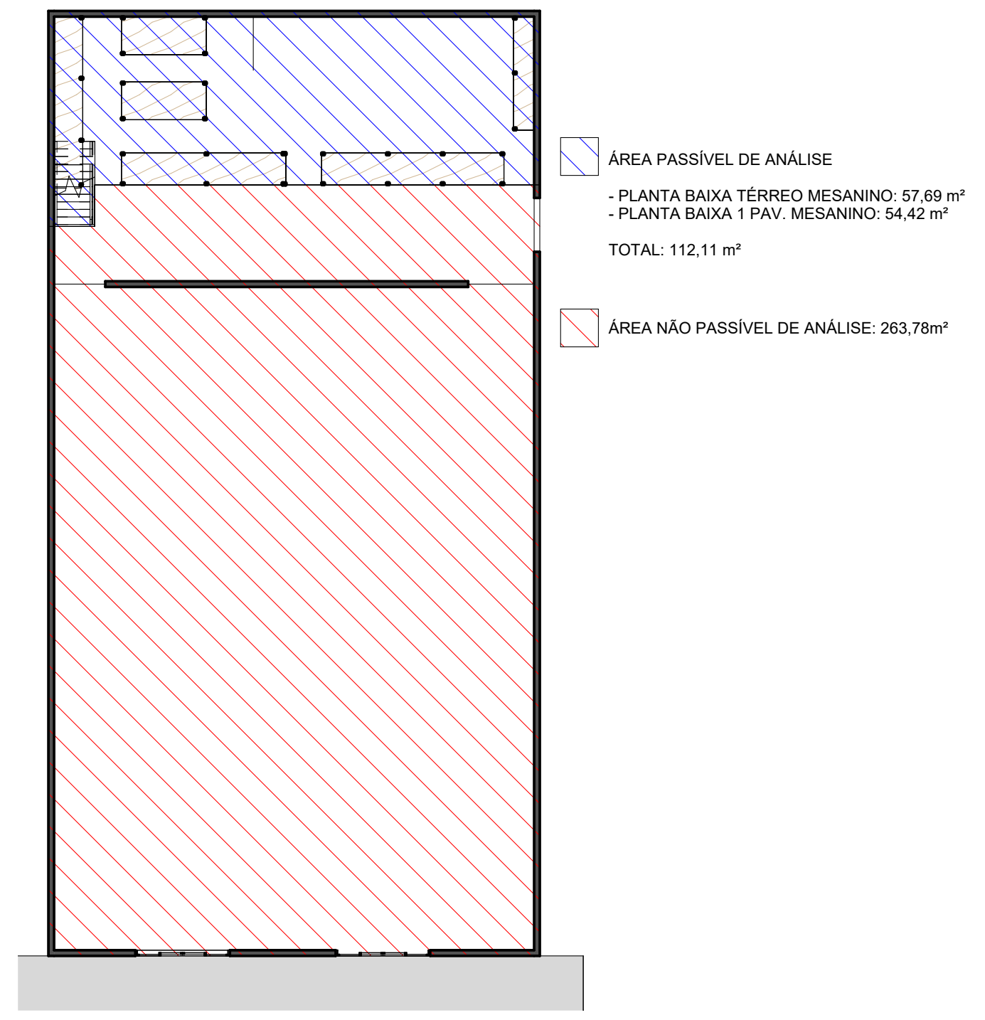
ÁREA PASSÍVEL DE ANÁLISE
- PLANTA BAIXA TÉRREO MESANINO: 57,69 m²
- PLANTA BAIXA 1 PAV. MESANINO: 54,42 m²
TOTAL: 112,11 m²
ÁREA NÃO PASSÍVEL DE ANÁLISE: 263,78m²

10 PLANTA DE ÁREAS

1 : 200

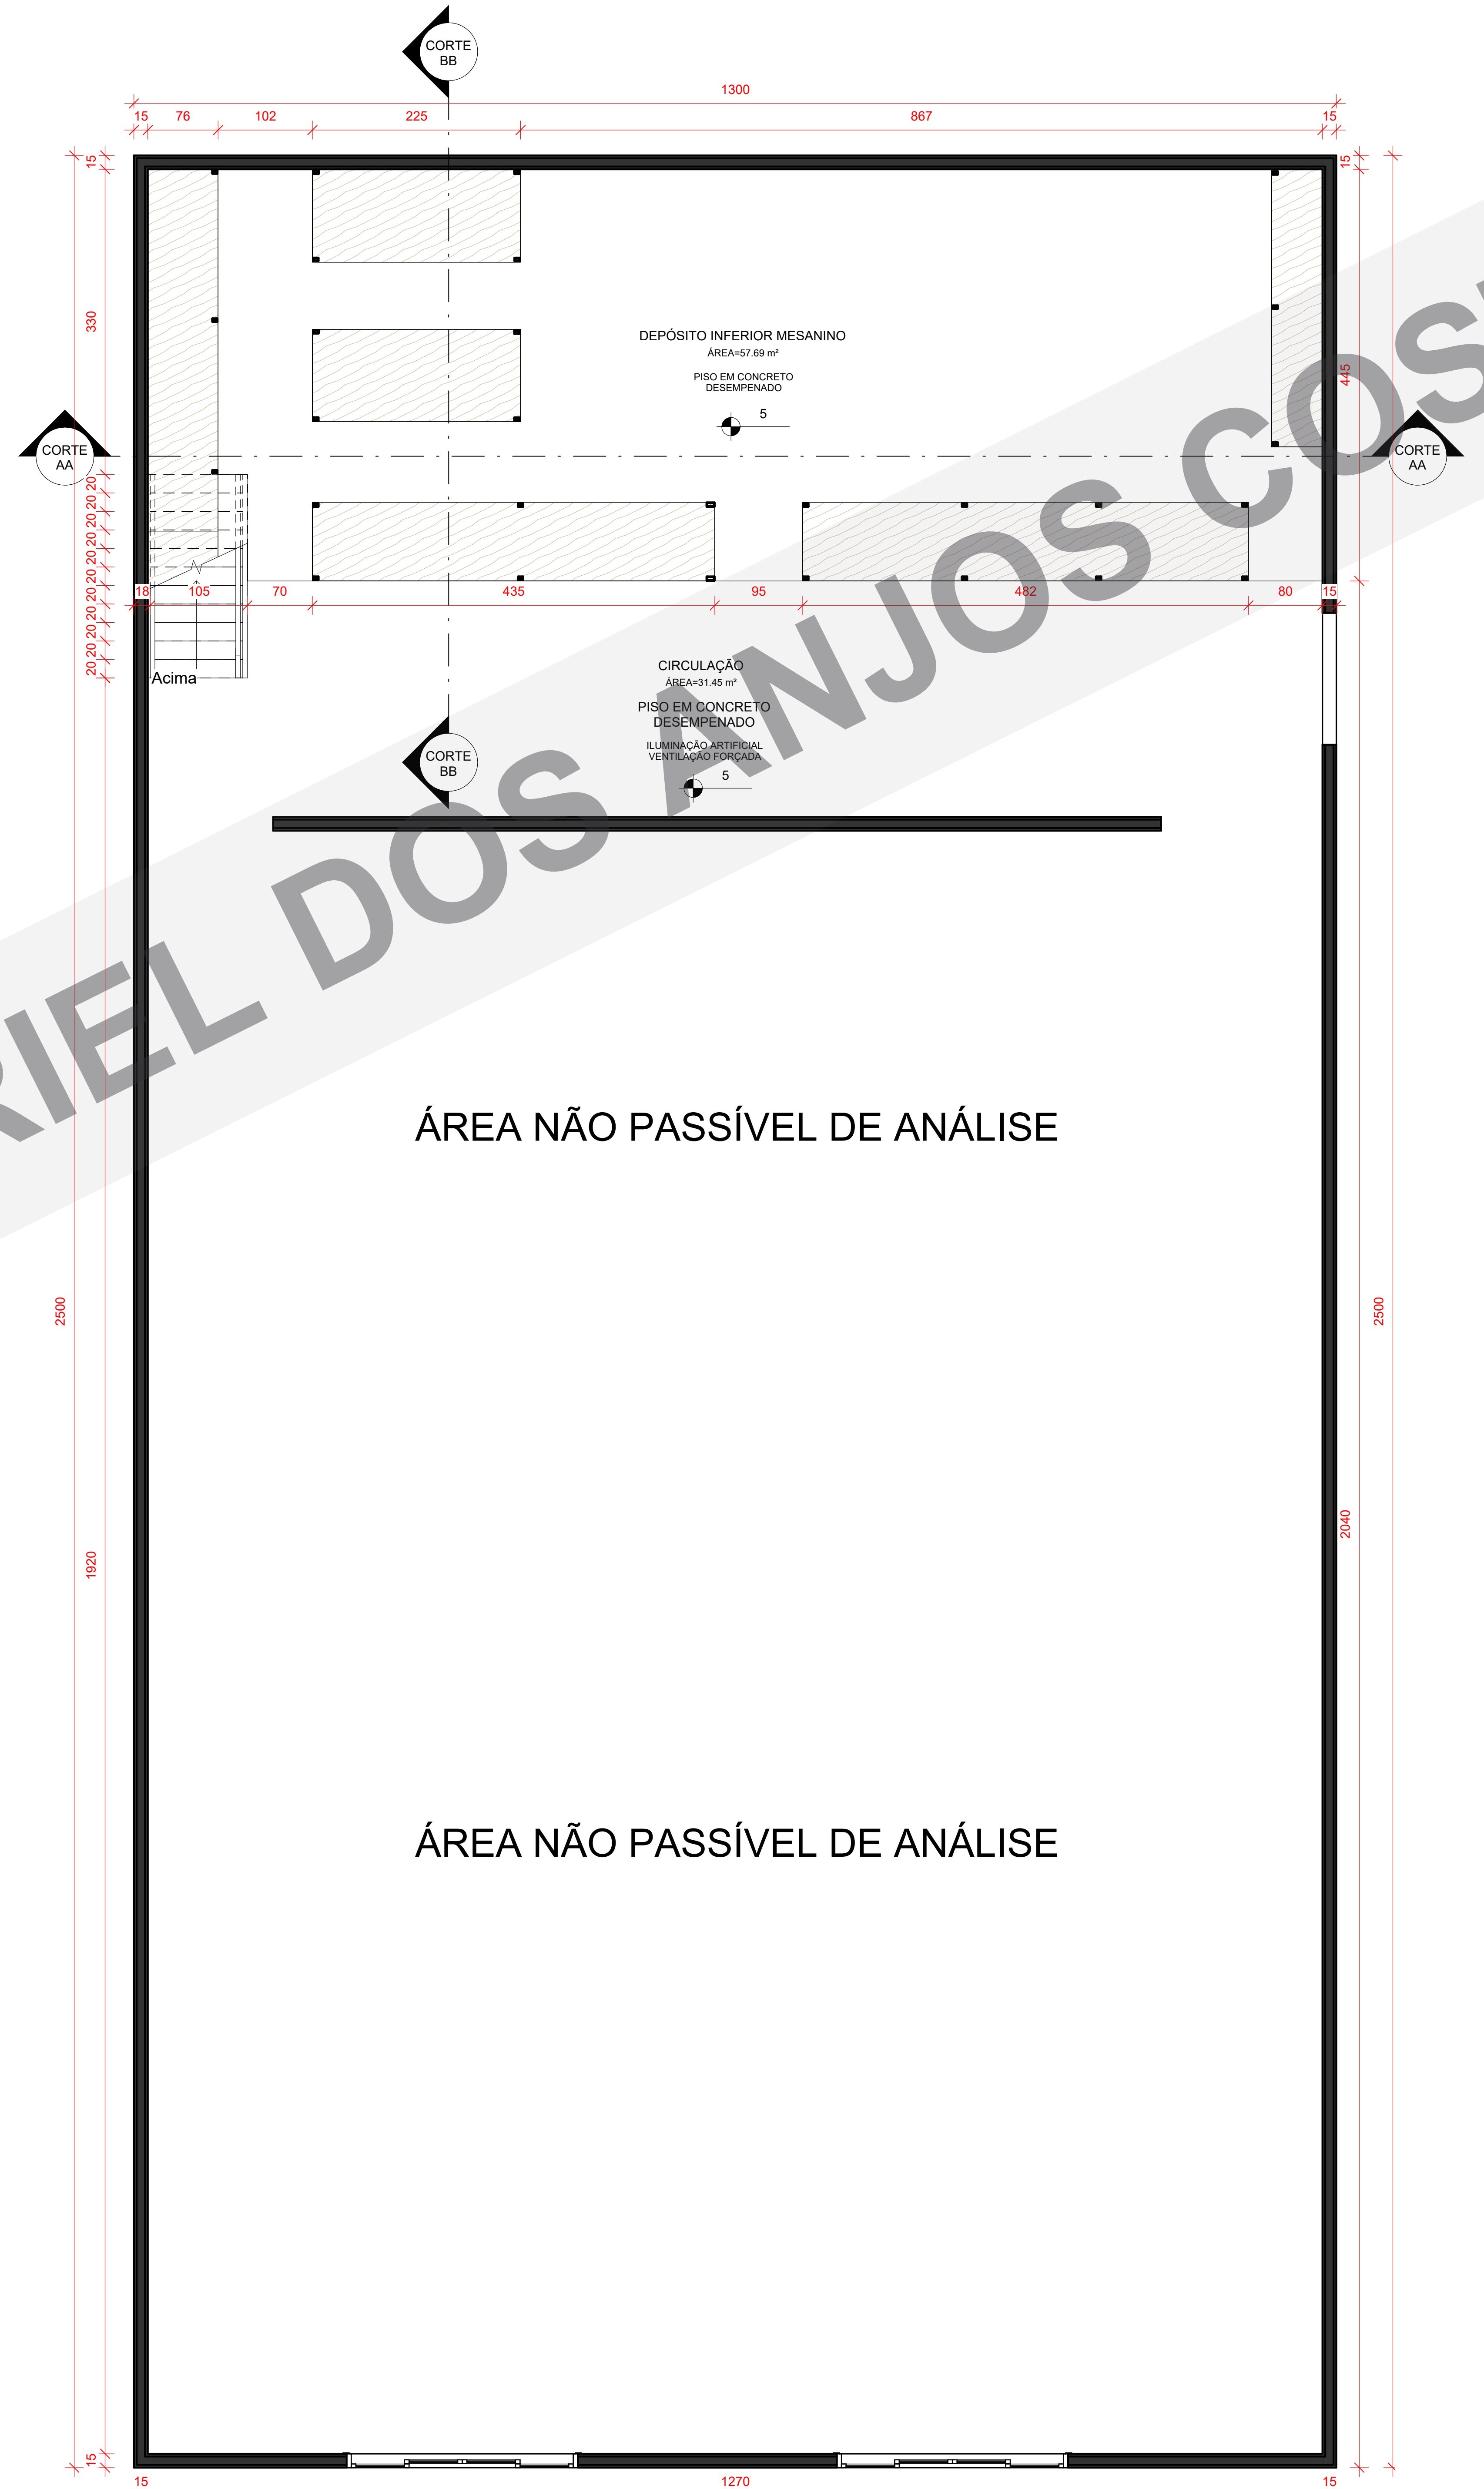
CORTE
BB
1300
15
76
102
225
867
15
15
330
445
CORTE
AA
CORTE
AA
DEPÓSITO INFERIOR MESANINO
ÁREA=57.69 m²
PISO EM CONCRETO
DESEMPENADO
5
20 20 20 20 20 20 20 20 20 20 20
18
105
70
435
95
482
80
15
Acima
CIRCULAÇÃO
ÁREA=31.45 m²
PISO EM CONCRETO
DESEMPENADO
ILUMINAÇÃO ARTIFICIAL
VENTILAÇÃO FORÇADA
5
CORTE
BB
ÁREA NÃO PASSÍVEL DE ANÁLISE
ÁREA NÃO PASSÍVEL DE ANÁLISE
2500
1920
2500
2040
15
15
1270
15
1300

1 PLANTA BAIXA TÉRREO MESANINO

1 : 50

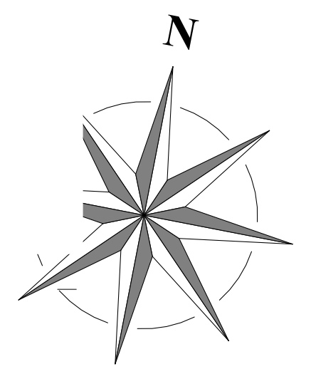

7 SITUAÇÃO

1 : 500

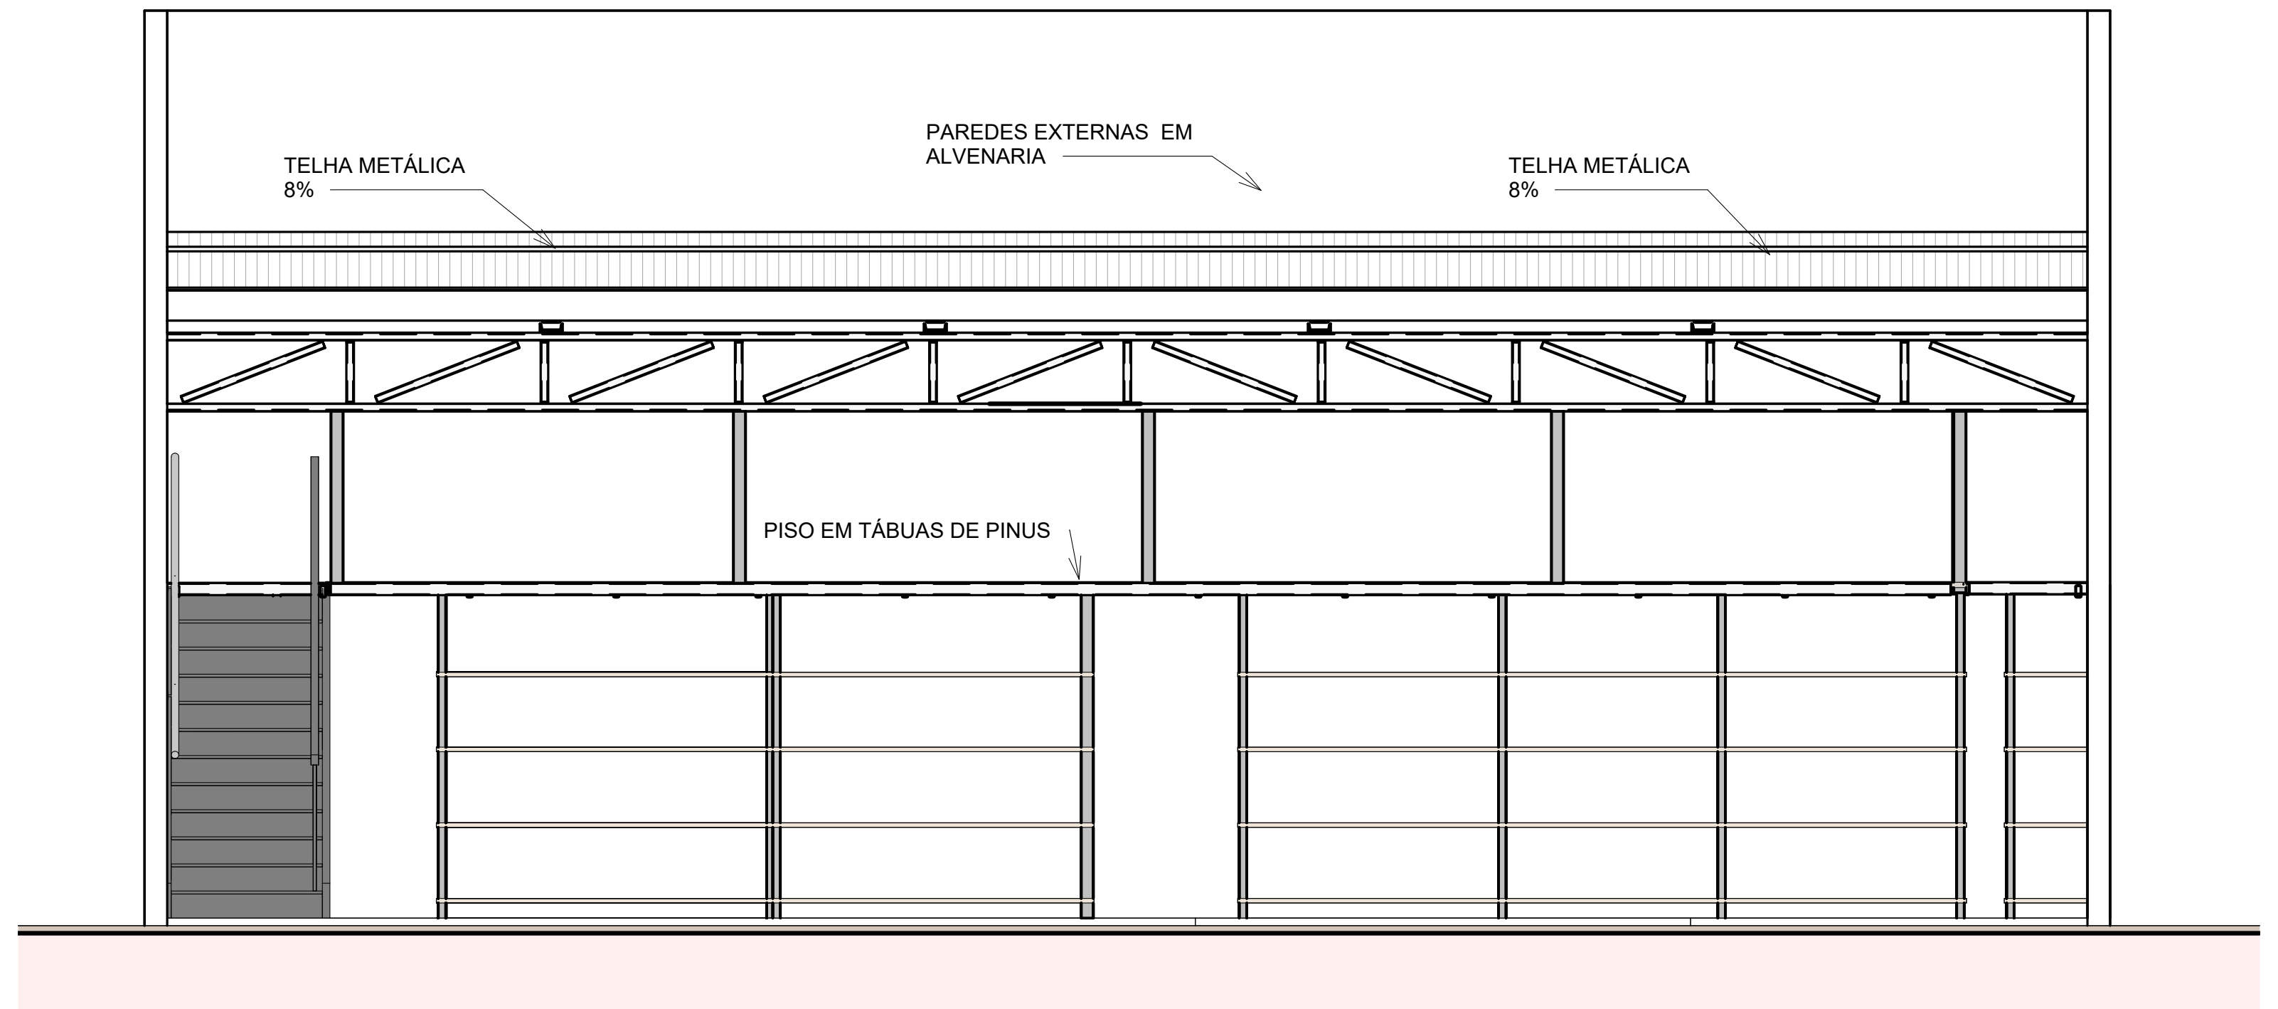
TELHA METÁLICA
8%
PAREDES EXTERNAS EM
ALVENARIA
TELHA METÁLICA
8%
PISO EM TÁBUAS DE PINUS

4 ELEVAÇÃO FRONTAL

1 : 50

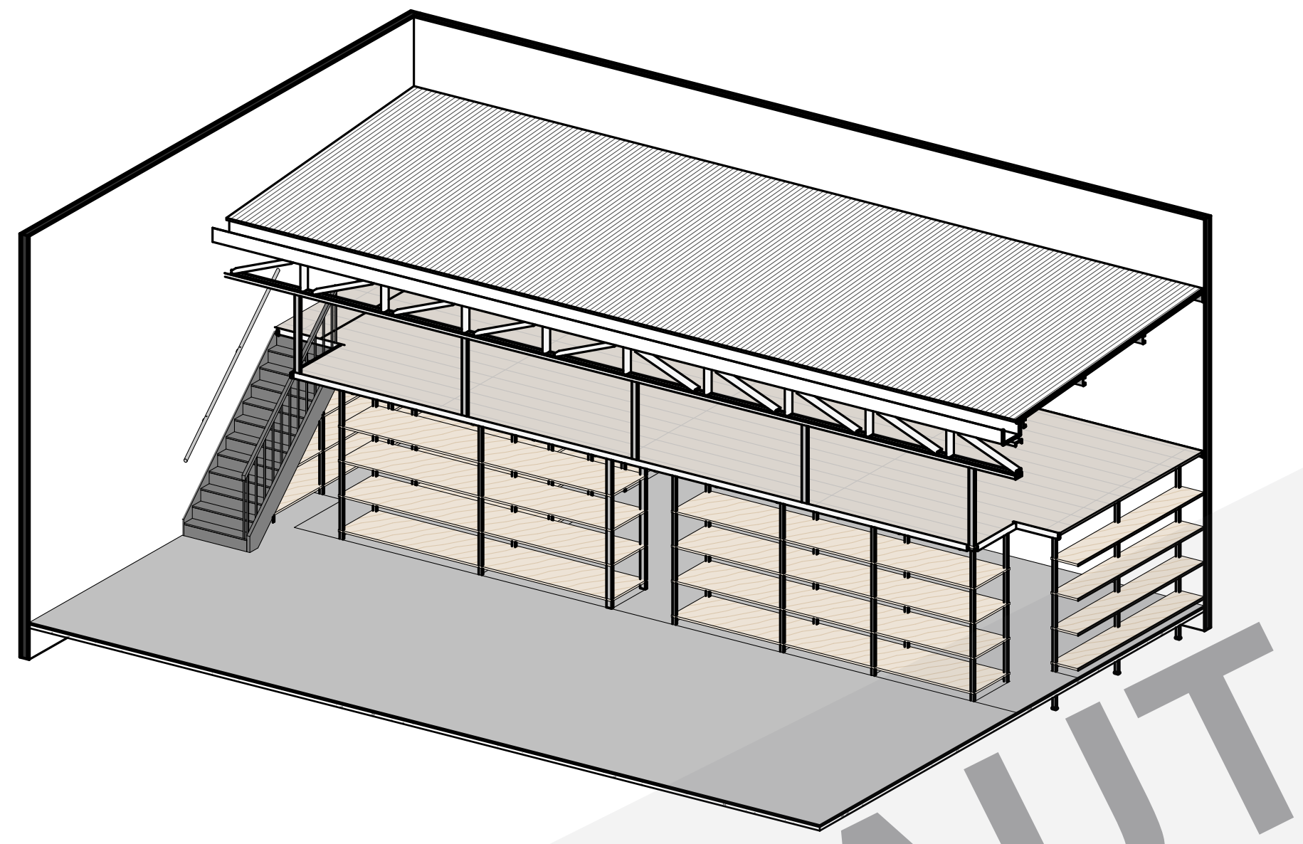

9 VISTA 3D

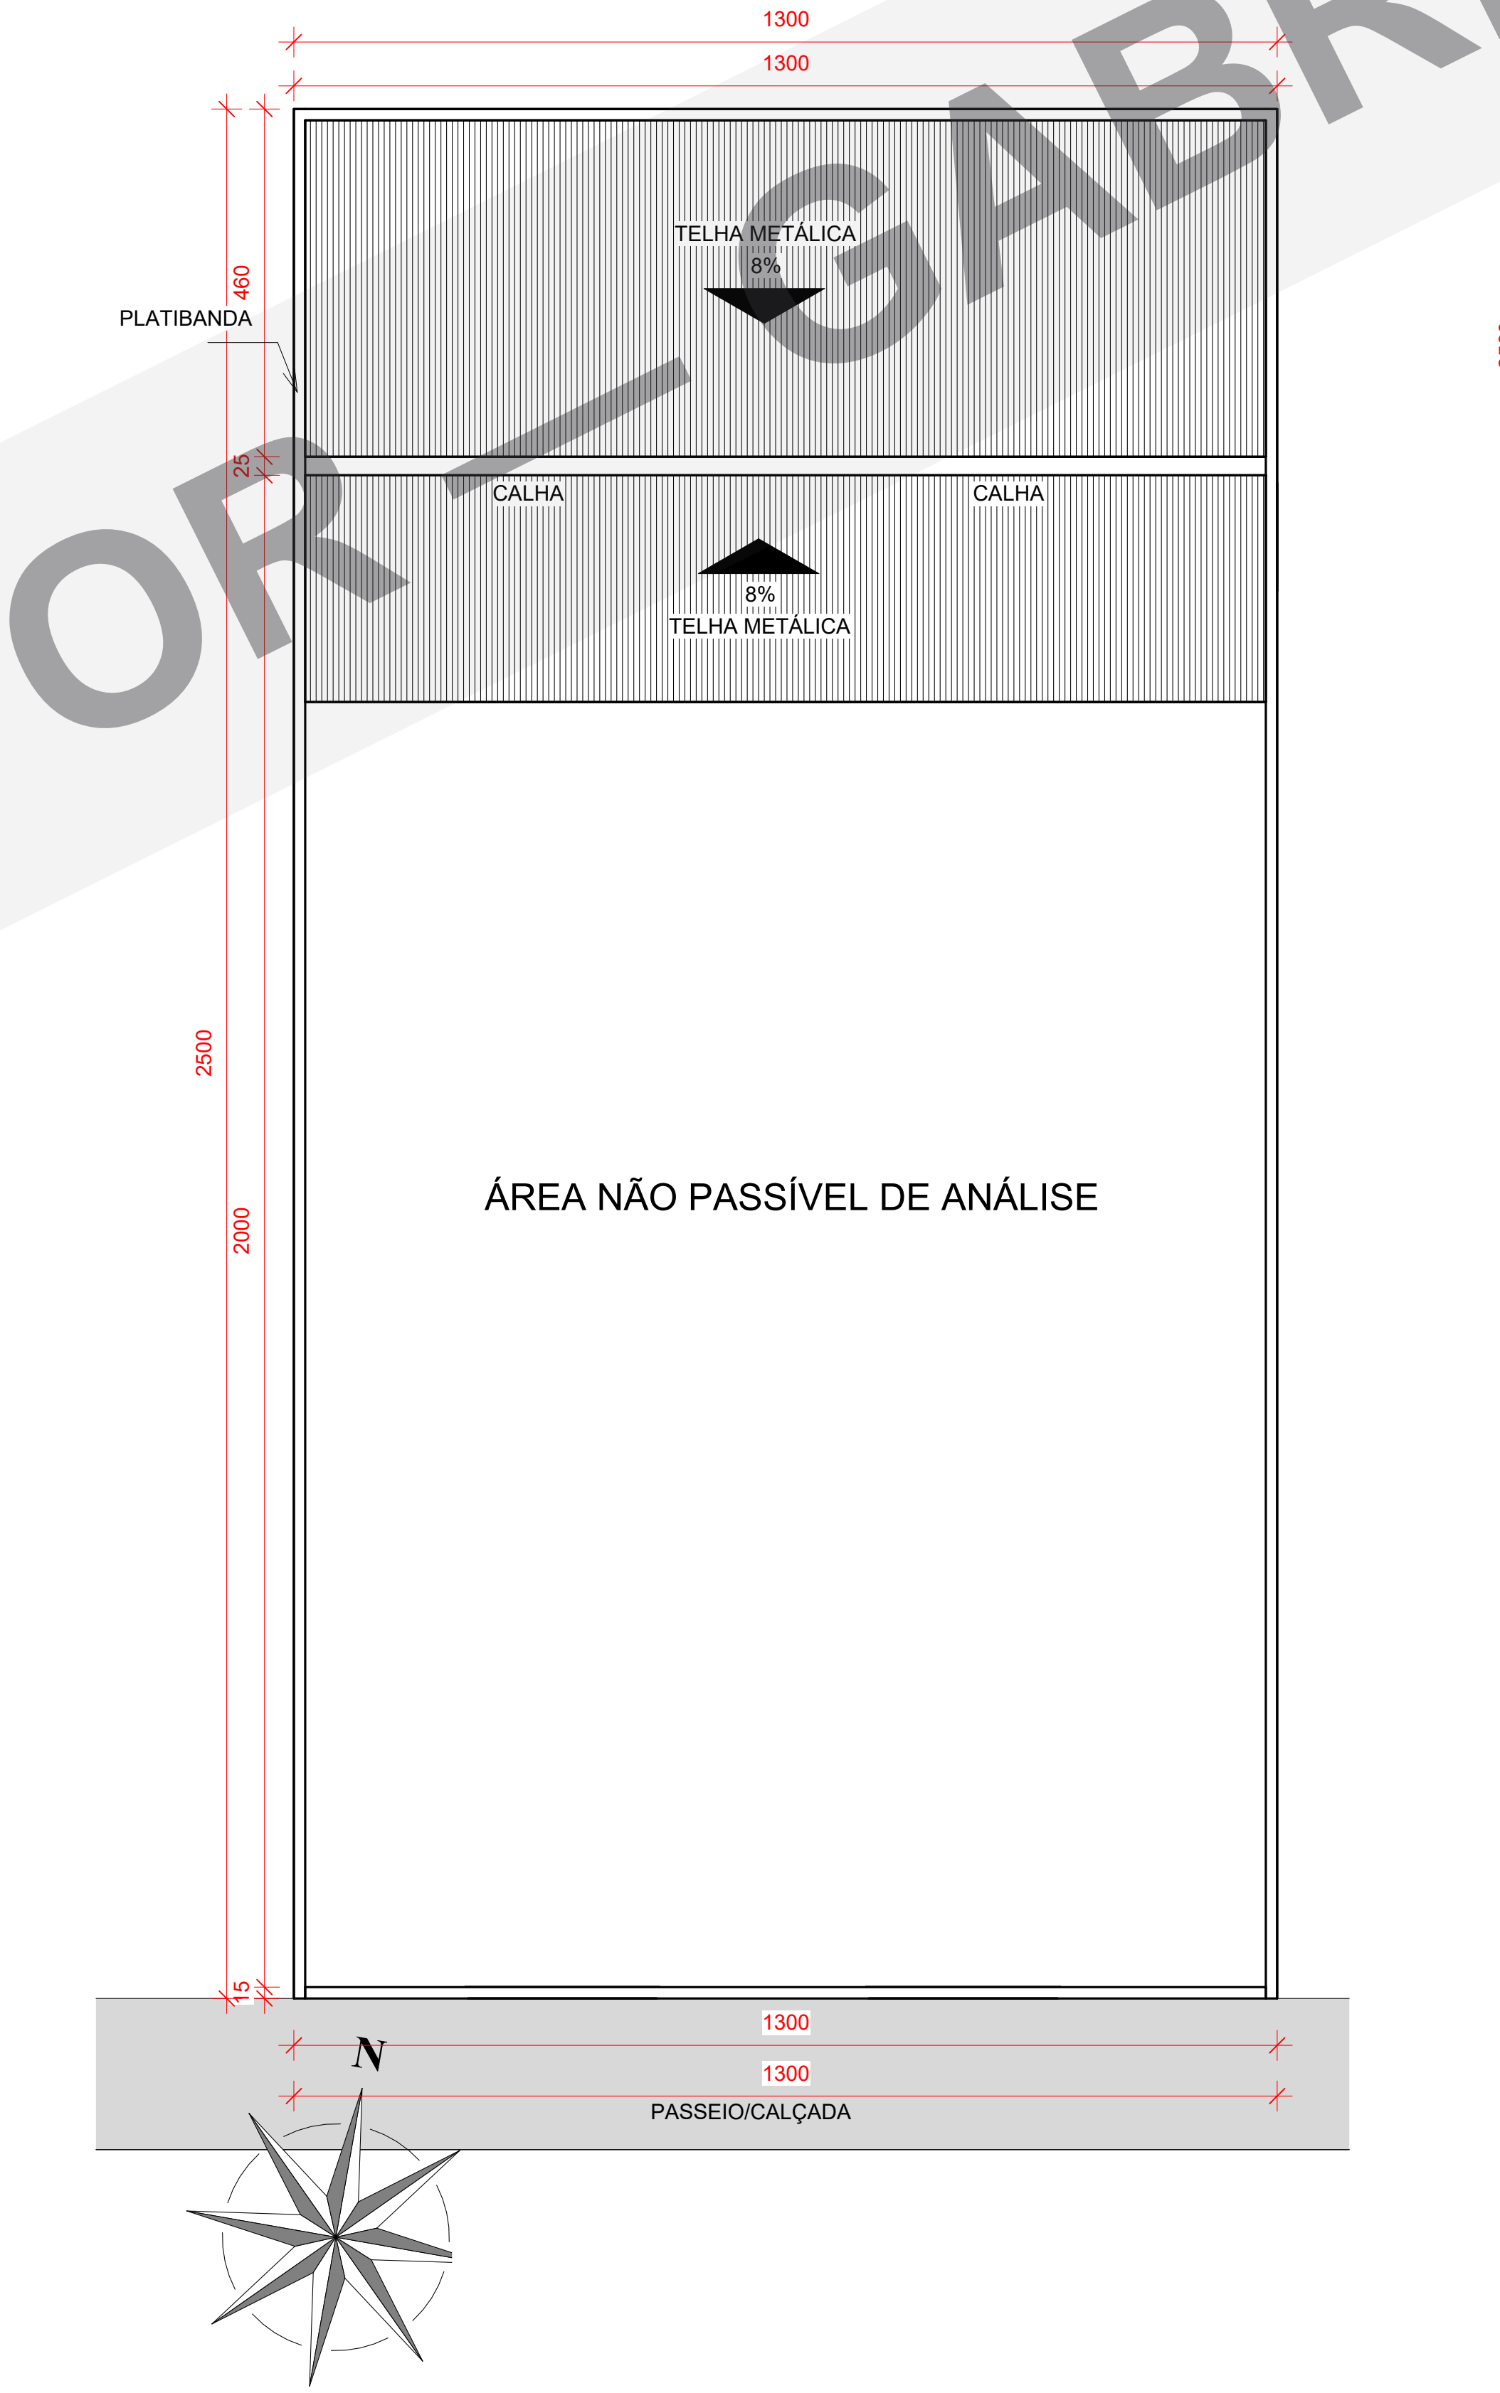
1300
1300
PLATIBANDA
460
25
TELHA METÁLICA
8%
CALHA
CALHA
8%
TELHA METÁLICA
ÁREA NÃO PASSÍVEL DE ANÁLISE
2500
2000
15
1300
1300
PASSEIO/CALÇADA
N

2 COBERTURA E LOCAÇÃO

1 : 100

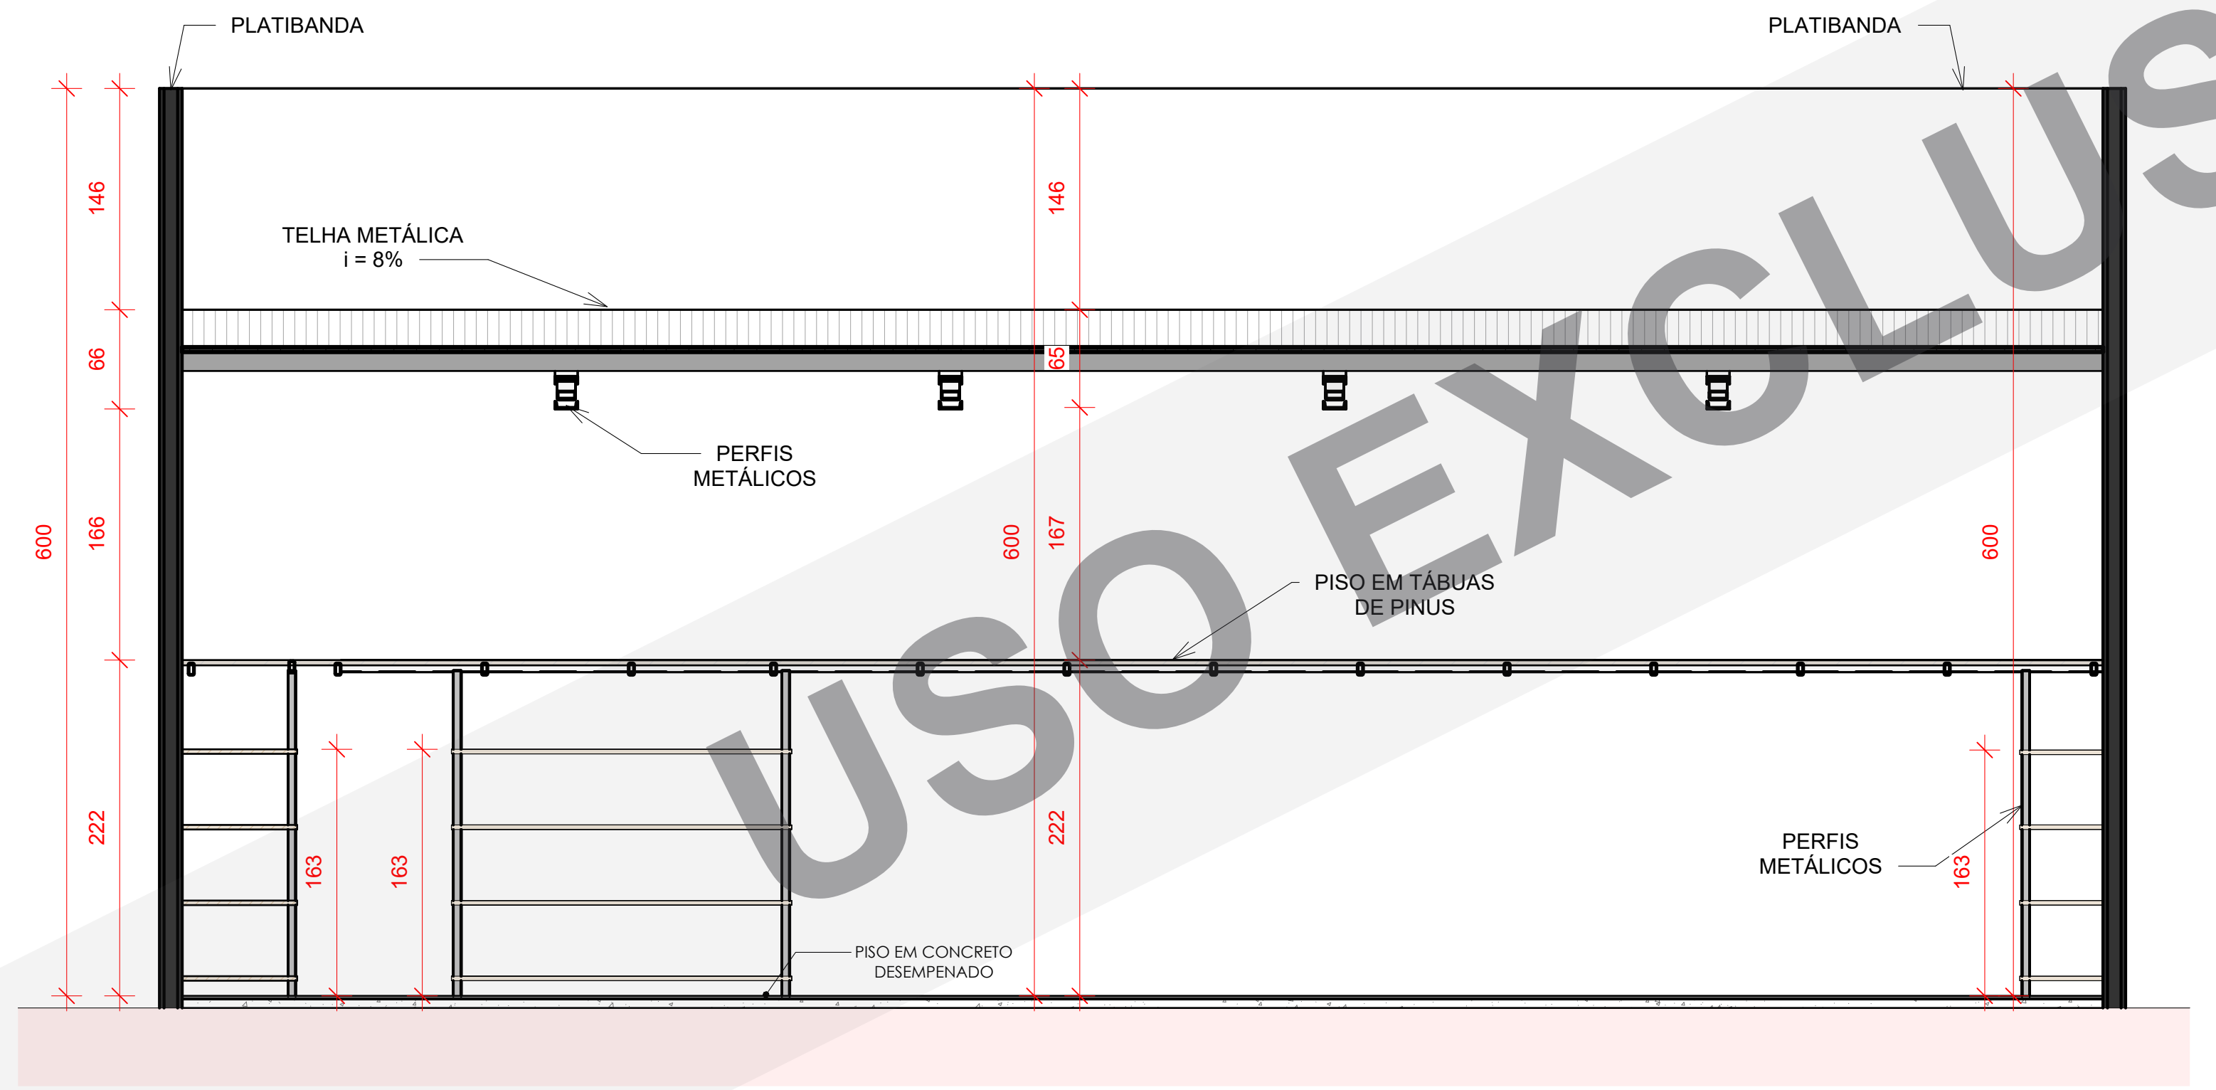
PLATIBANDA
PLATIBANDA
146
66
166
222
600
TELHA METÁLICA
i = 8%
146
65
167
600
222
PERFIS
METÁLICOS
PISO EM TÁBUAS
DE PINUS
163
163
PERFIS
METÁLICOS
163
600
PISO EM CONCRETO
DESEMPENADO

6 CORTE AA

1 : 50

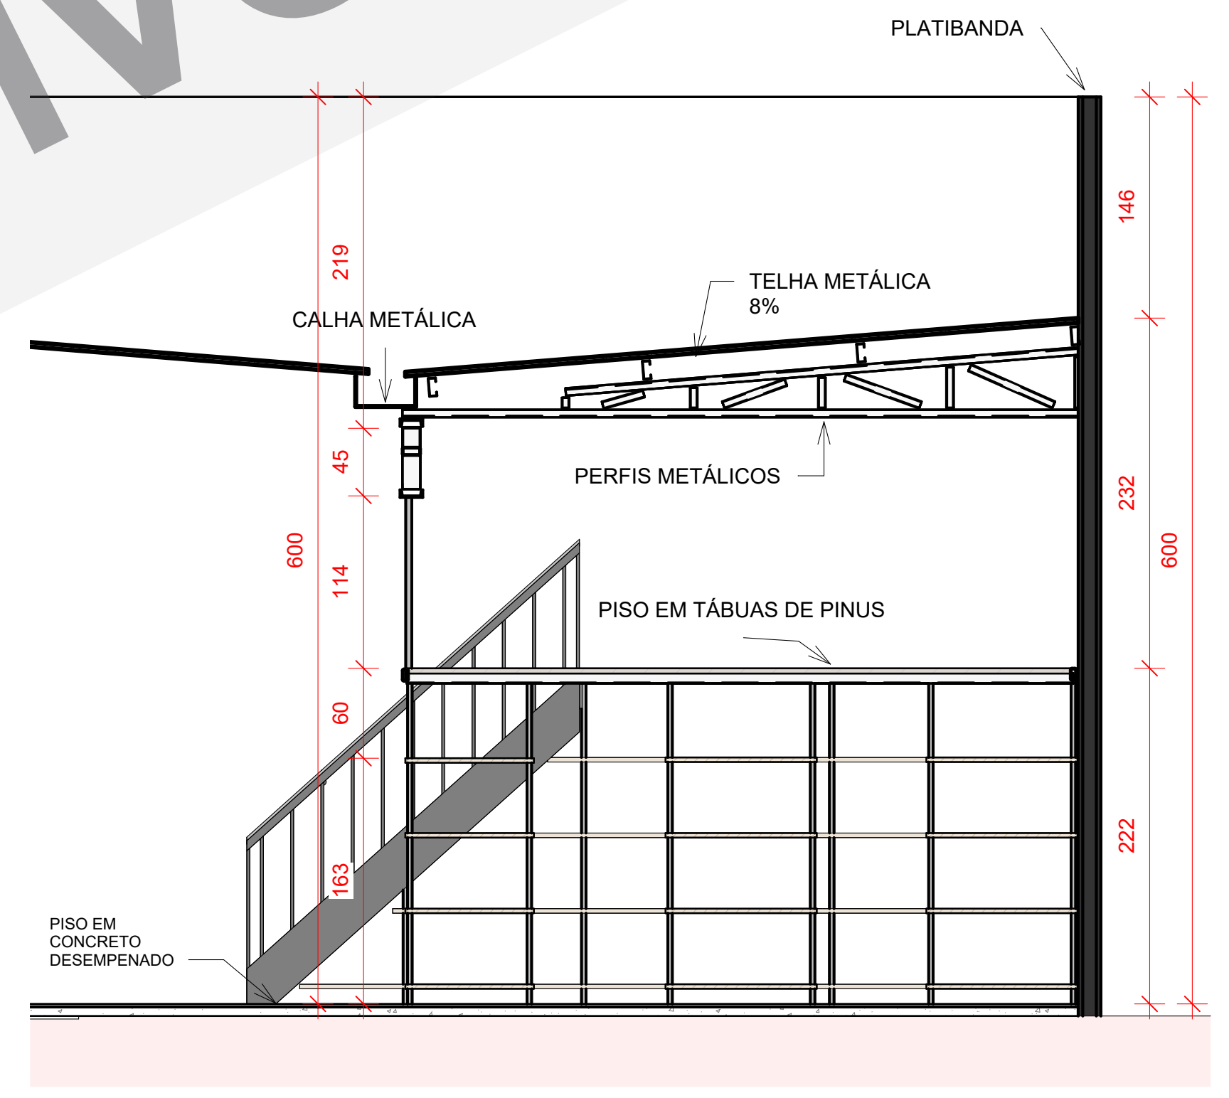
PLATIBANDA
219
CALHA METÁLICA
TELHA METÁLICA
8%
PERFIS METÁLICOS
45
114
60
163
600
PISO EM TÁBUAS DE PINUS
PISO EM
CONCRETO
DESEMPENADO
146
232
222
600

8 CORTE BB

1 : 50

USO EXCLUSIVO DO AUTOR — GABRIEL DOS ANJOS COSTA