

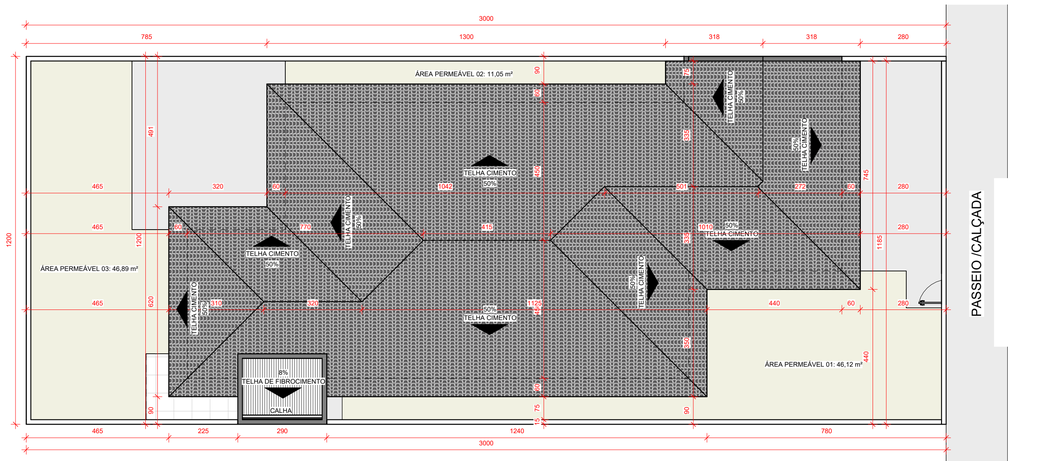


2 COBERTURA E LOCAÇÃO
1 : 100

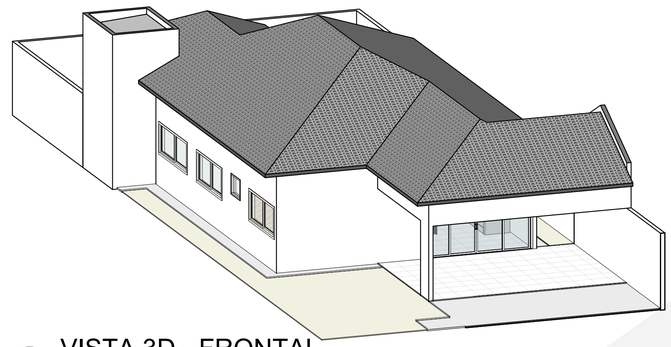

3 VISTA 3D - FRONTAL

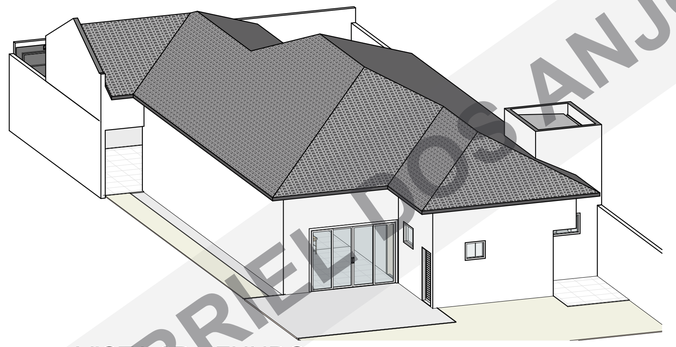

4 VISTA 3D - FUNDO




5
1 : 500

QUADRO DE JANELAS

CÓDIGO	LARGURA	ALTURA	A. PEITORIL	TIPO / MATERIAL	QUANT.
J1	240	100	110	CORRER 2F/VIDRO	2
J2	90	70	150	BASCULANTE/VIDRO	2
J3	70	60	150	BASCULANTE/VIDRO	1
J4	270	100	110	CORRER 2F/VIDRO	1
J5	100	70	150	BASCULANTE/VIDRO	1

QUADRO DE PORTAS

CÓDIGO	LARGURA	ALTURA	TIPO / MATERIAL	QUANT.
P1	642	250	BASCULANTE/FERRO	1
P2	380	210	CORRER 4F/VIDRO TEMPERADO	1
P3	300	210	CORRER 4F/VIDRO TEMPERADO	1
P4	70	210	ABRIR/MADEIRA	4
P5	80	210	CORRER/1F MADEIRA	3
P6	80	180	ABRIR/METAL	2
P7	80	210	ABRIR/MADEIRA	3

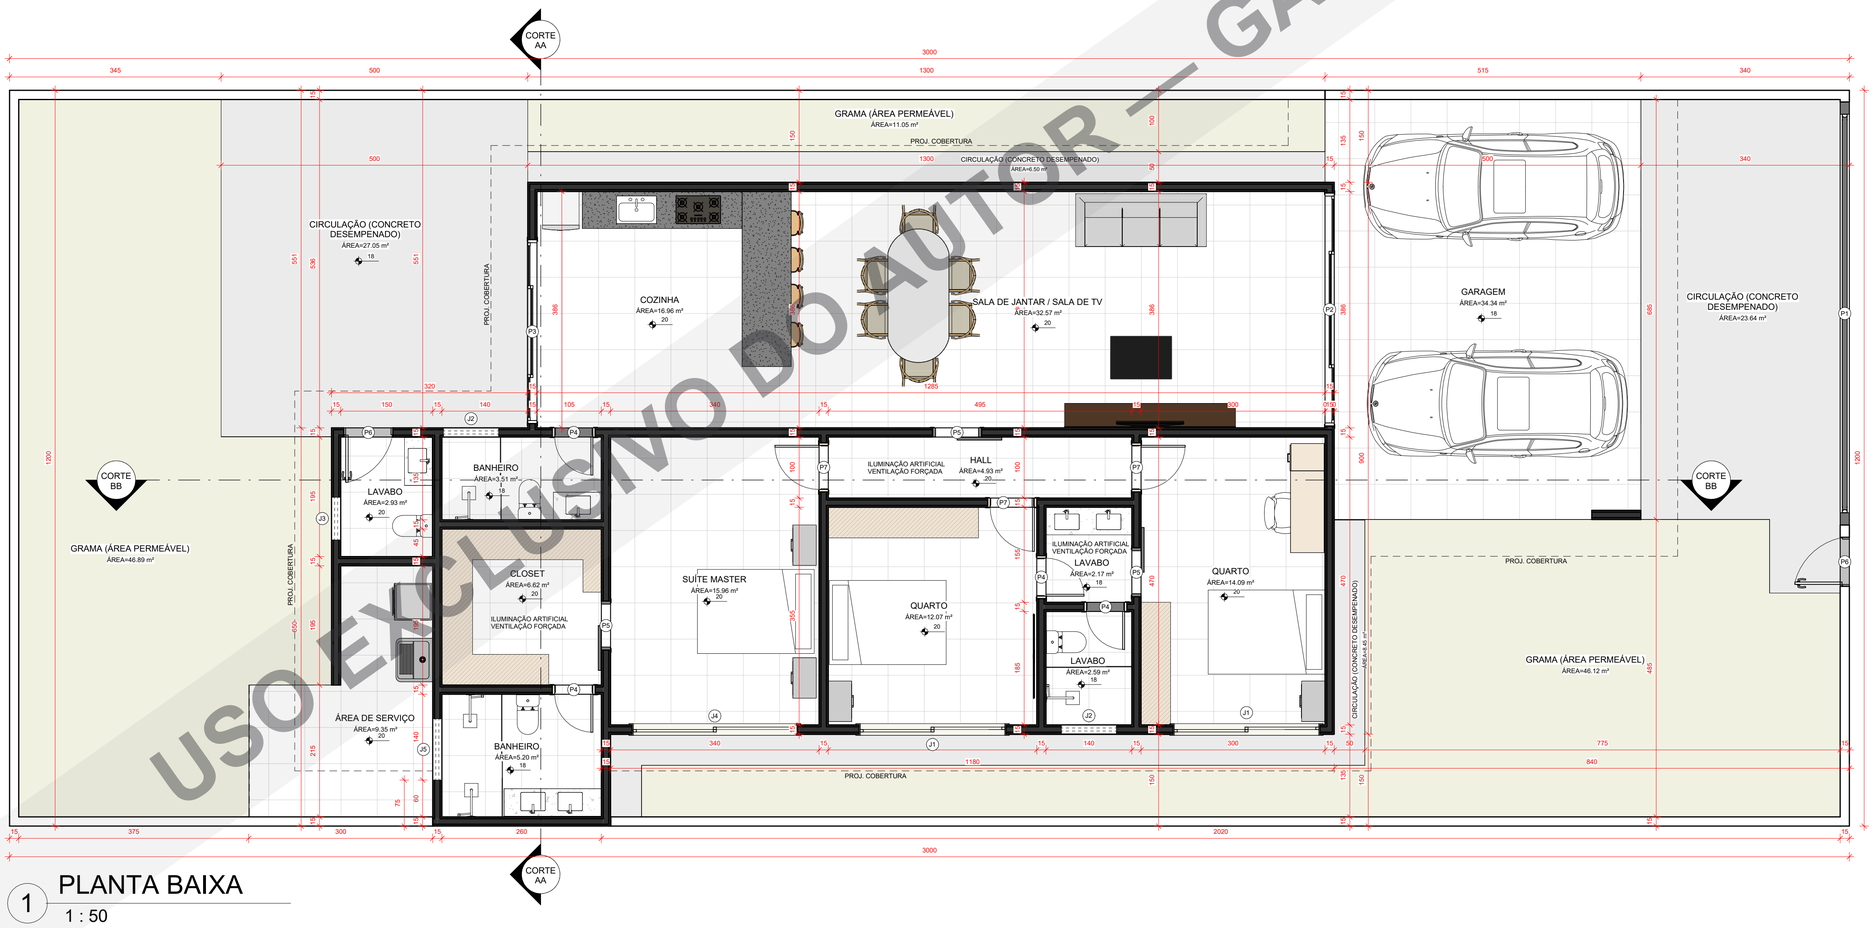

1 PLANTA BAIXA
1 : 50

USO EXCLUSIVO DO AUTOR – GABRIEL DOS ANJOS COSTA